



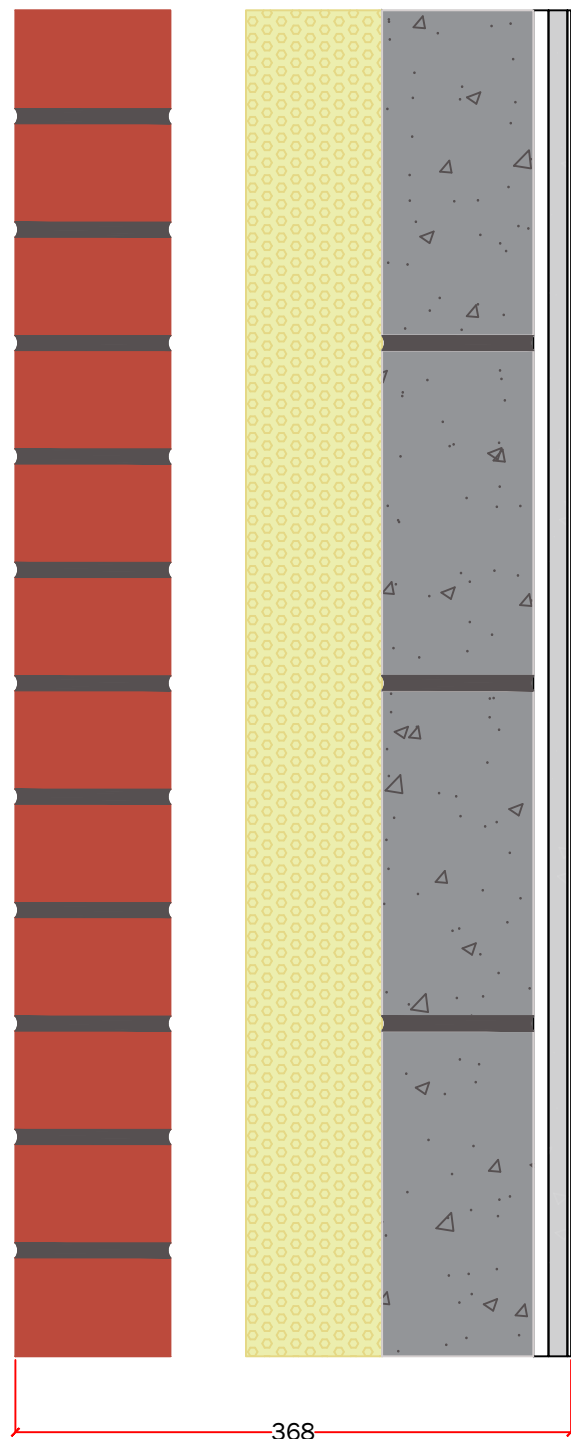

Traditional brick and block wall

Brickwork-102.5mm
Cavity-50mm
Insulation-90mm
Blockwork-100mm
Dot & dab-10mm
Plasterboard-12.5mm
Skim-2.5mm


TOTAL: 367.5mm
u-Value: 0.18W/m²K

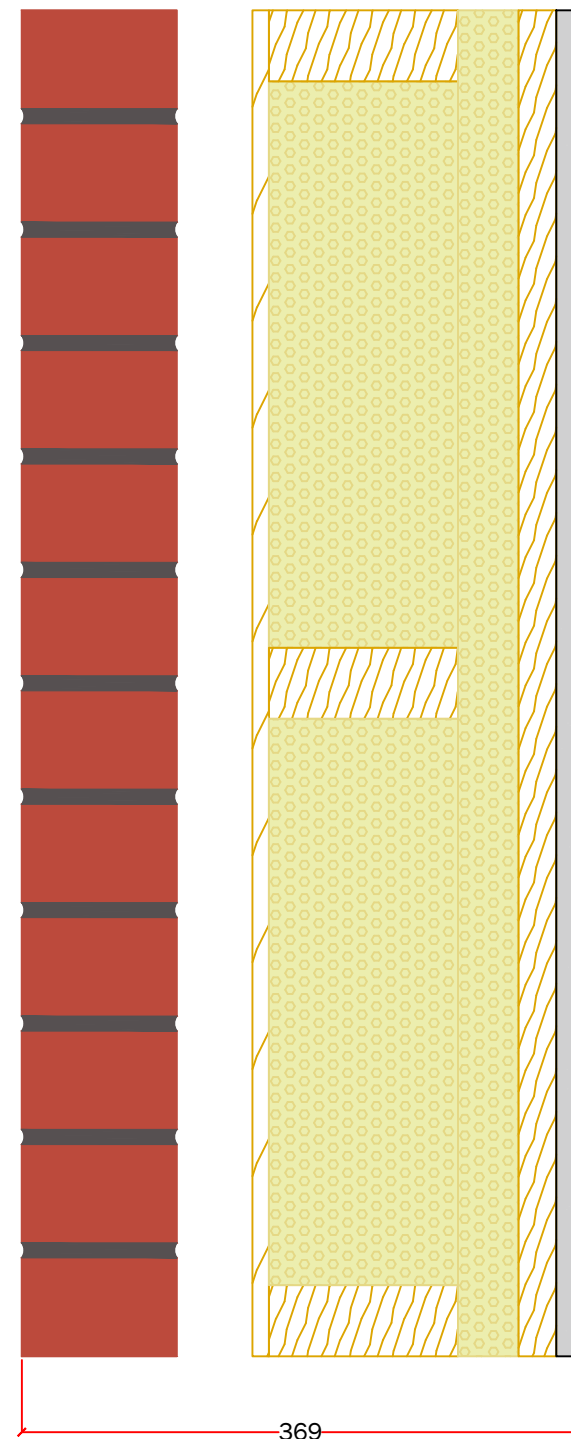

Traditional brick and timber frame wall

Brickwork-102.5mm
Cavity-50mm
OSB-11mm
Stud work (insulated)-120mm
Insulation-40mm
Battens-25mm
Plasterboard-12.5mm
Skim-2.5mm

TOTAL: 368.5mm
u-Value: 0.18W/m²K

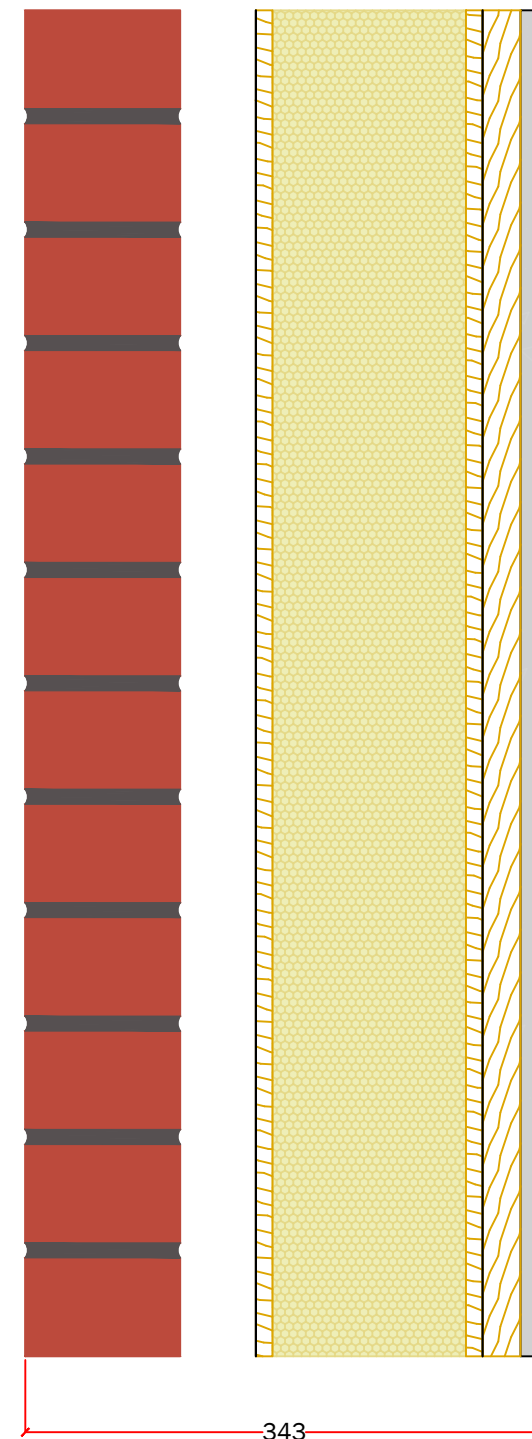


Traditional brick and SIP wall

Brickwork-102.5mm
Cavity-50mm
SIPs*-150mm
Battens-25mm
Plasterboard-12.5mm
Skim-2.5mm

TOTAL: 342.5mm
u-Value: 0.16W/m²K

*GlideVale TF200 thermo membrane
exterior and VCL interior, thickness
negligible

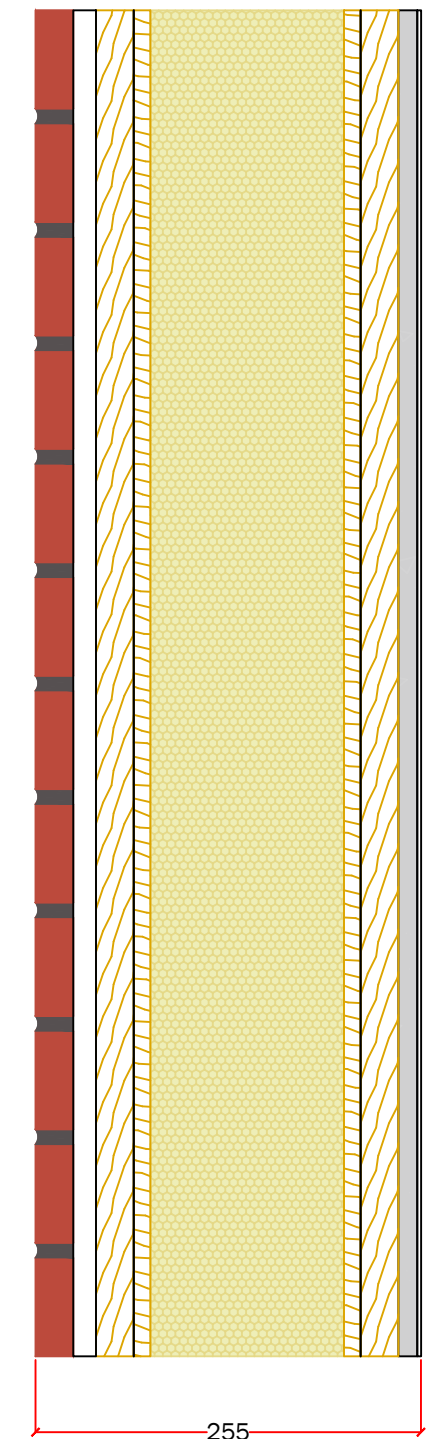


Brick slip and SIP wall

Brick slip-20mm
Carrier board-15mm
Battens-25mm
SIPs*-150mm
Battens-25mm
Plasterboard-12.5mm
Skim-2.5mm

TOTAL: 255mm
u-Value: 0.16W/m²K


*GlideVale TF200 thermo membrane
exterior and VCL interior, thickness
negligible

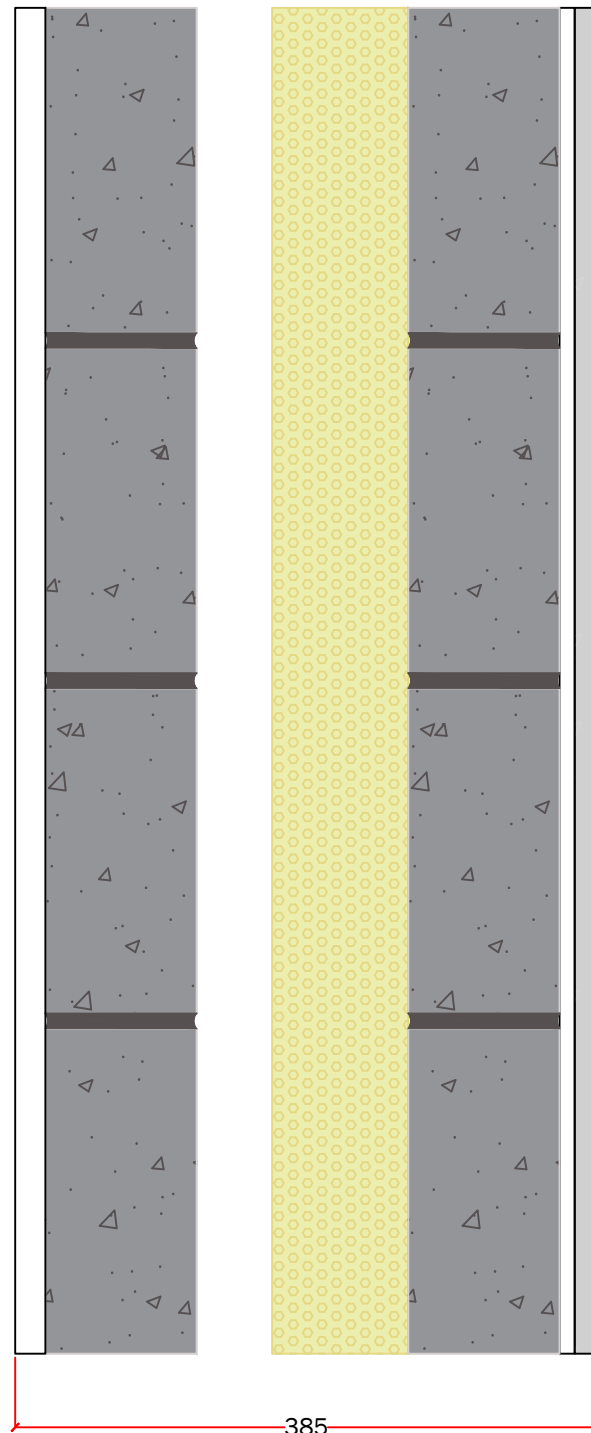

Render onto block wall

Render-20mm
Blockwork-100mm
Cavity-50mm
Insulation-90mm
Blockwork-100mm
Dot & dab-10mm
Plasterboard-12.5mm
Skim-2.5mm


TOTAL: 385mm
u-Value: 0.18W/m²K

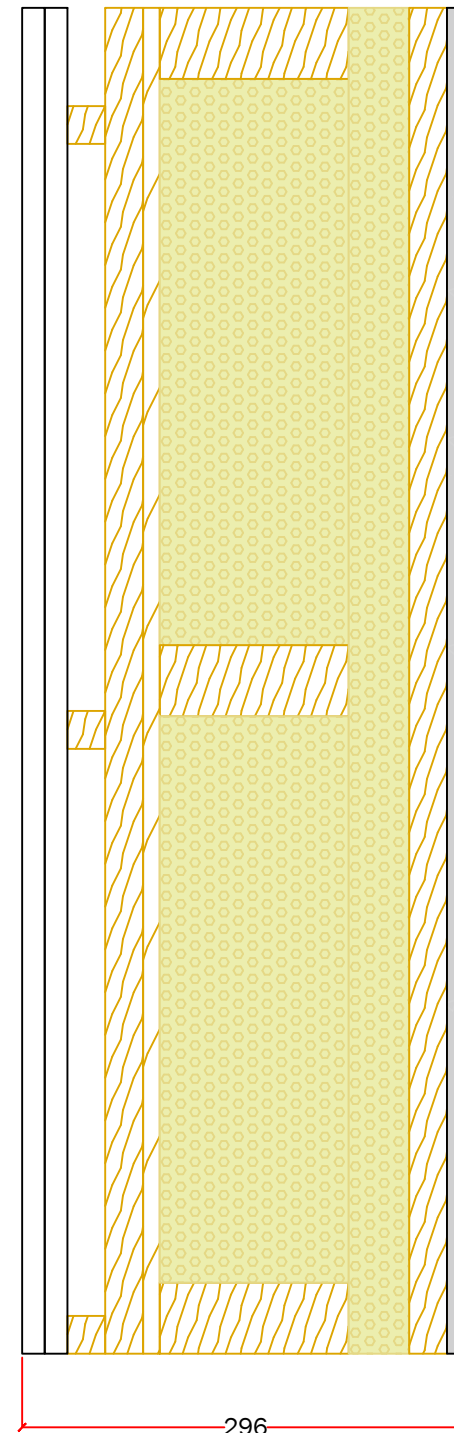

Render onto timber frame wall

Render-15mm
Carrier board-15mm
Cross batten-50mm
OSB-11mm
Stud work (insulated)-120mm
Insulation-40mm
Battens-25mm
Plasterboard-12.5mm
Skim-2.5mm

TOTAL: 296mm
u-Value: 0.18W/m²K

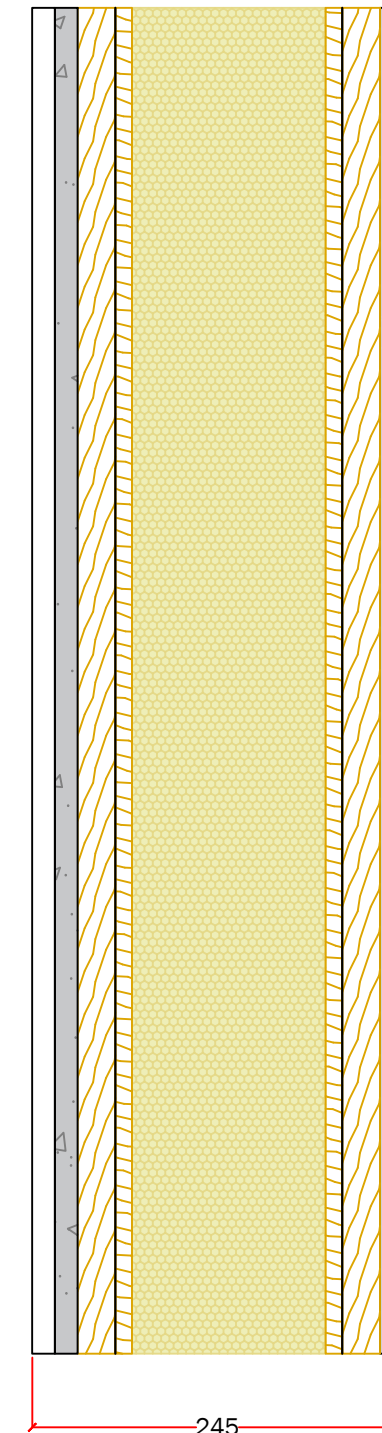


Render and SIP wall

Render-15mm
Carrier board-15mm
Battens-25mm
SIPs*-150mm
Battens-25mm
Plasterboard-12.5mm
Skim-2.5mm

TOTAL: 245mm
u-Value: 0.16W/m²K


*GlideVale TF200 thermo membrane
exterior and VCL interior, thickness
negligible

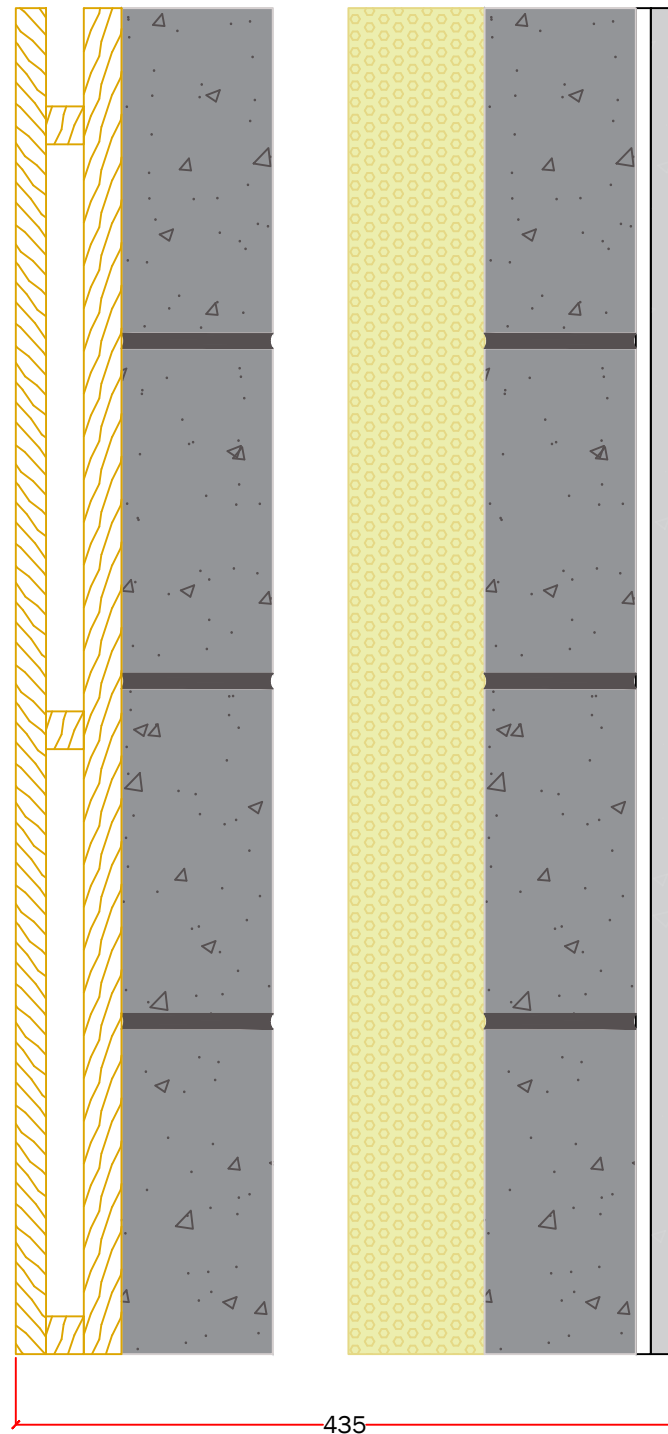

Timber cladding onto block wall

Cladding-20mm
Cross batten-50mm
Blockwork-100mm
Cavity-50mm
Insulation-90mm
Blockwork-100mm
Dot & dab-10mm
Plasterboard-12.5mm
Skim-2.5mm


TOTAL: 435mm
u-Value: 0.18W/m²K

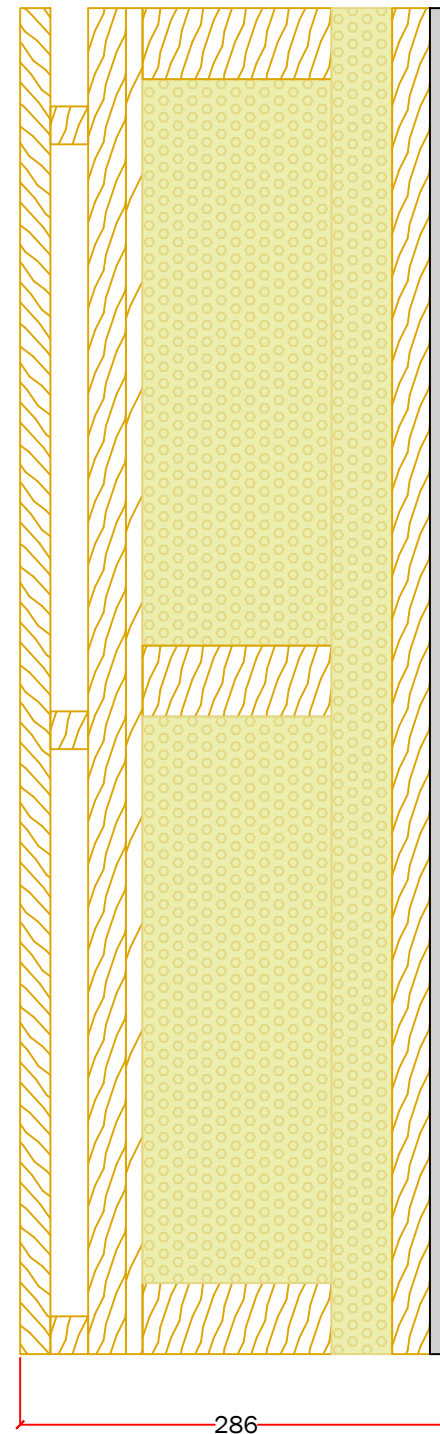

Timber cladding onto timber frame wall

Cladding-20mm
Cross batten-50mm
OSB-11mm
Stud work (insulated)-120mm
Insulation-40mm
Battens-25mm
Plasterboard-12.5mm
Skim-2.5mm

TOTAL: 286mm
u-Value: 0.18W/m²K

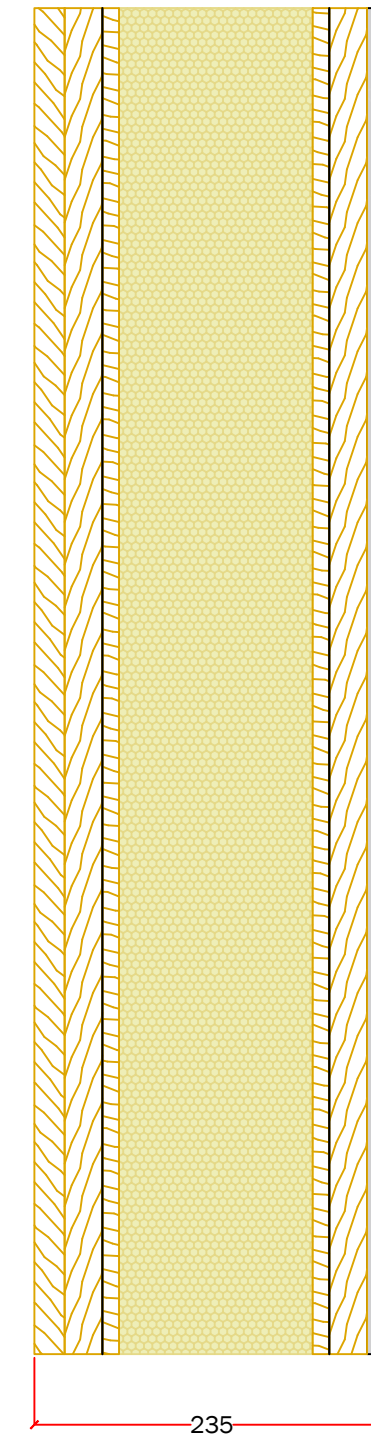


Timber cladding and SIP wall

Cladding-20mm
Battens-25mm
SIPs*-150mm
Battens-25mm
Plasterboard-12.5mm
Skim-2.5mm


TOTAL: 235mm
u-Value: 0.16W/m²K


*GlideVale TF200 thermo membrane
exterior and VCL interior, thickness
negligible

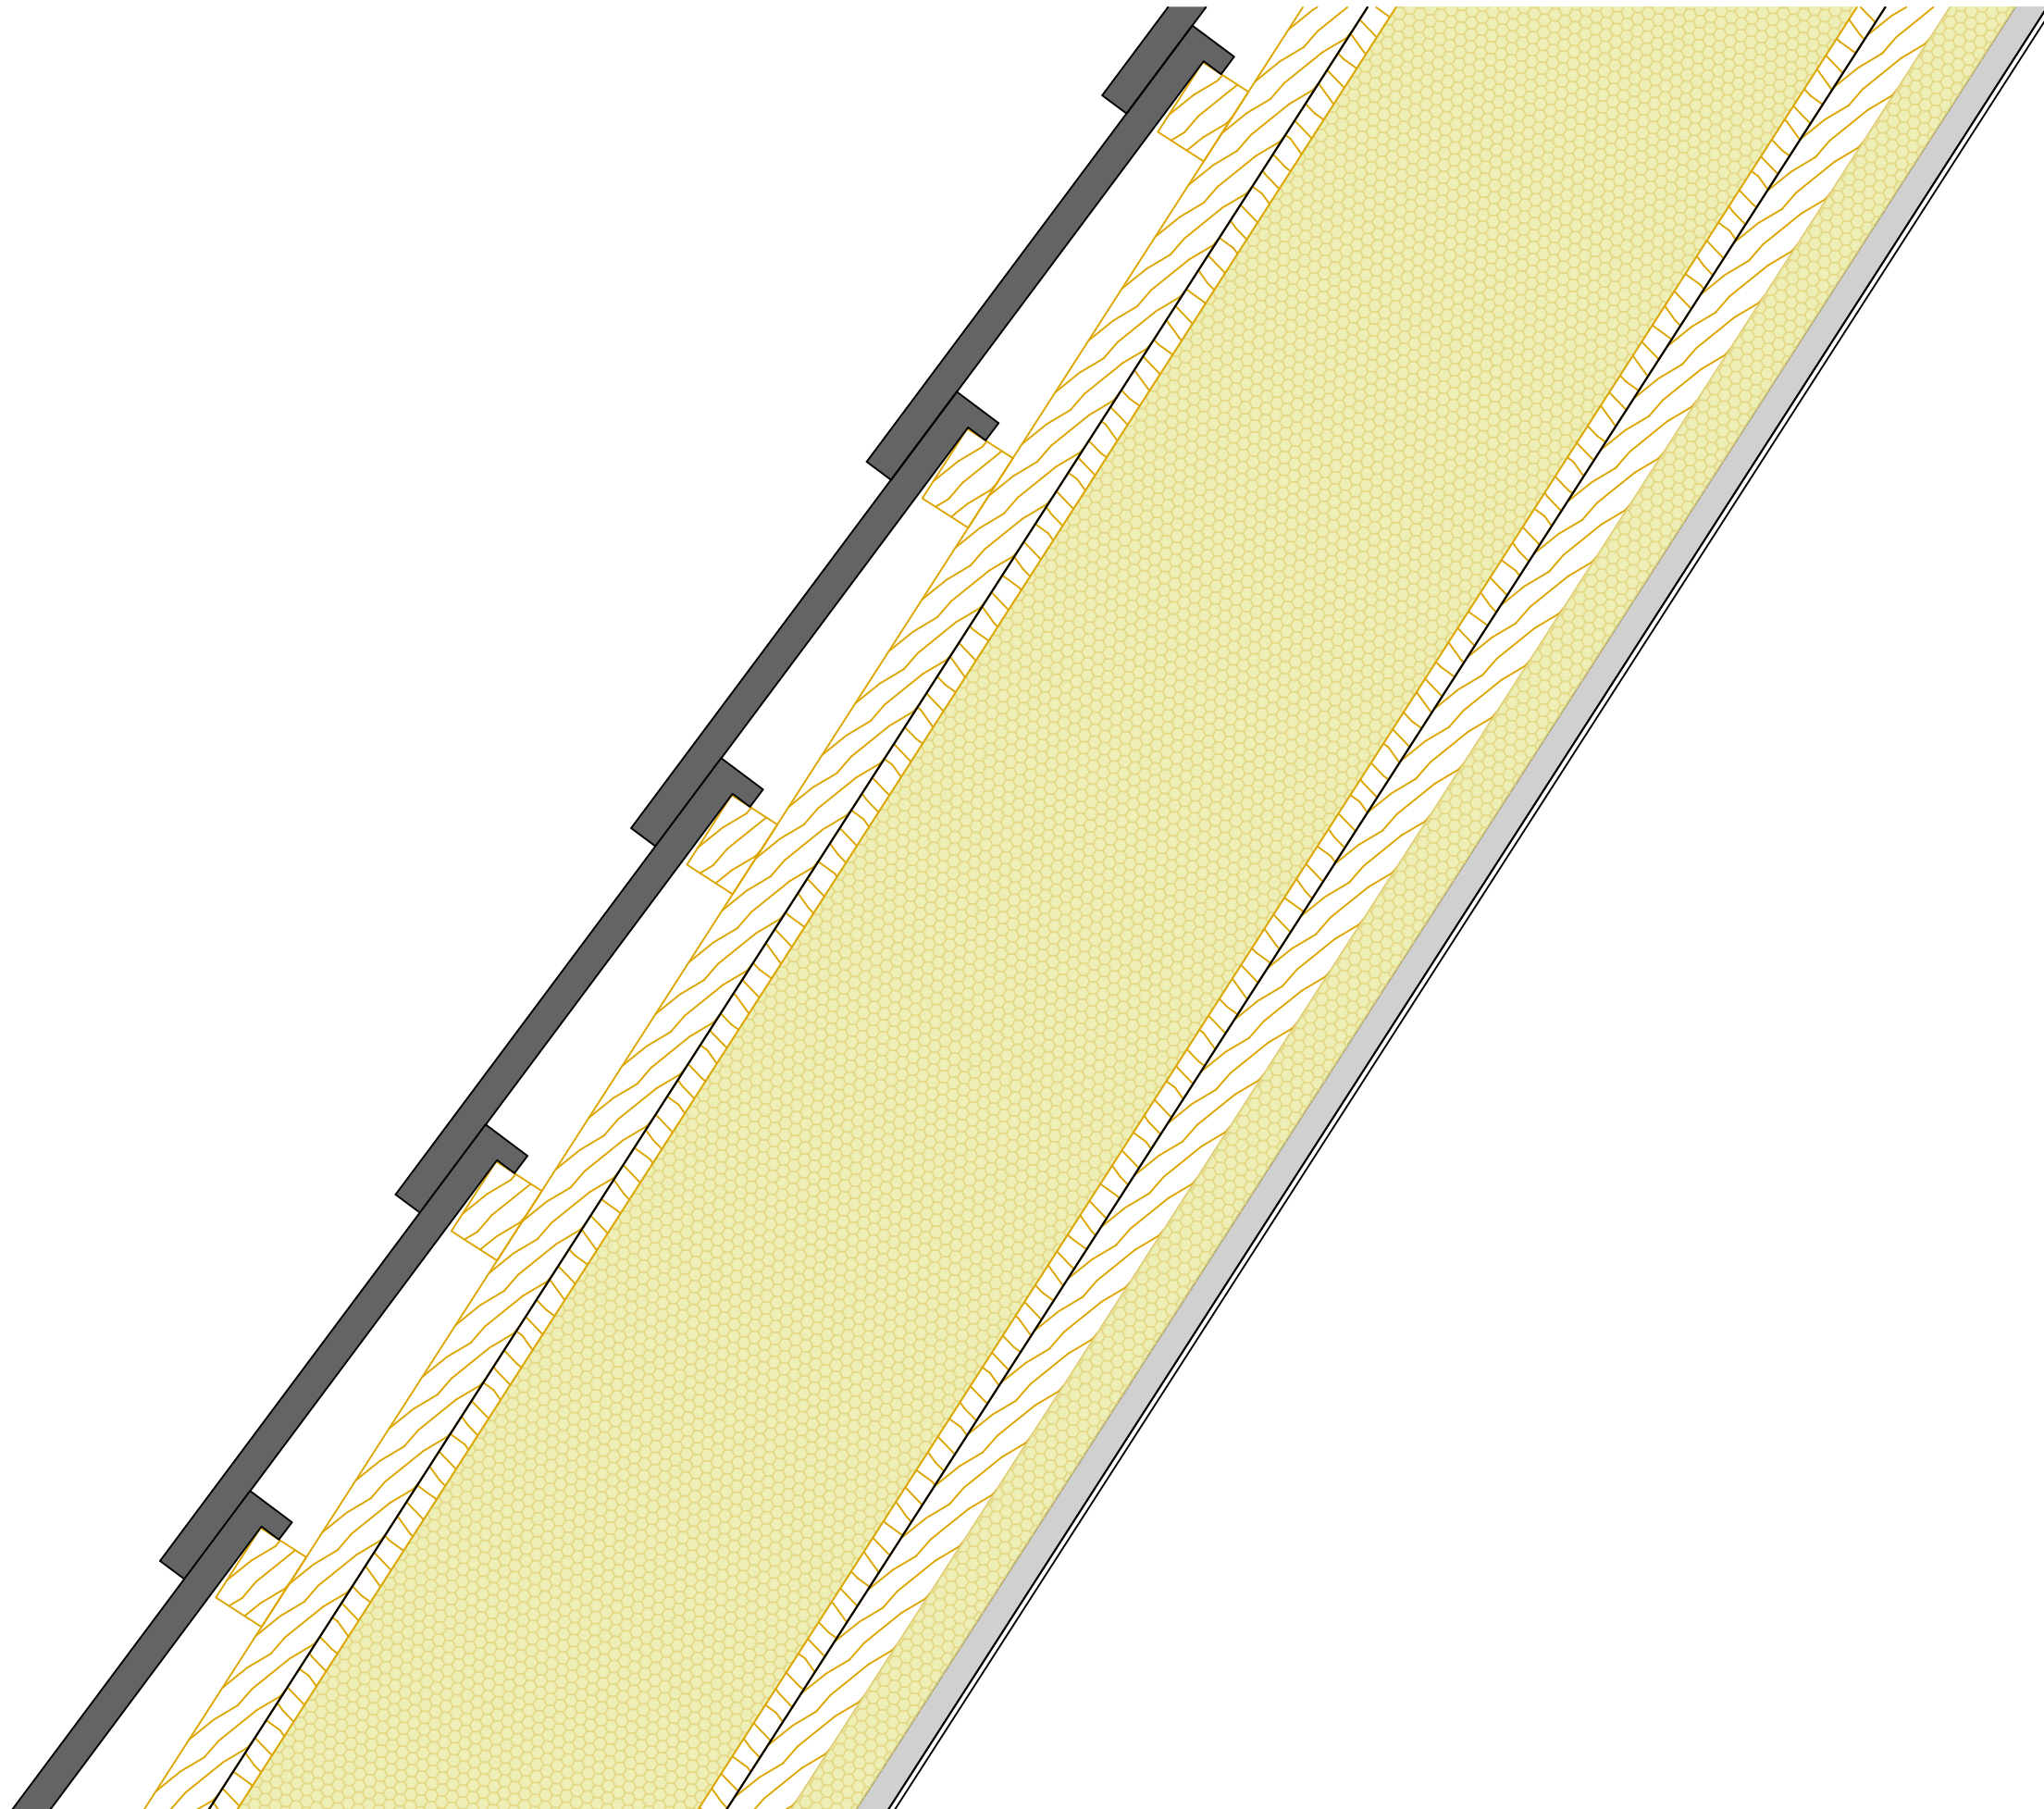

phone: 01590 642 087
e-mail: sales@newforestips.co.uk
web: www.newforestips.co.uk




200mm SIP ROOF STANDARD BUILD UP

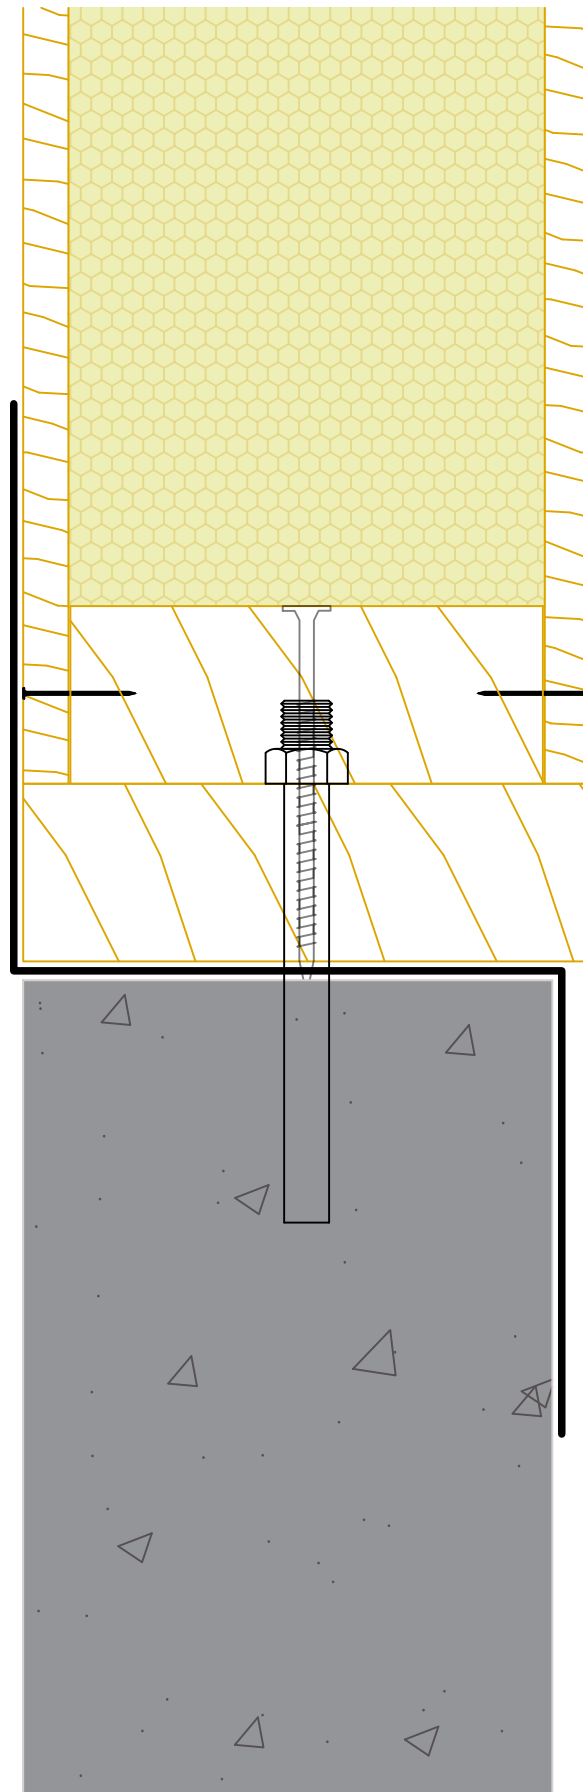

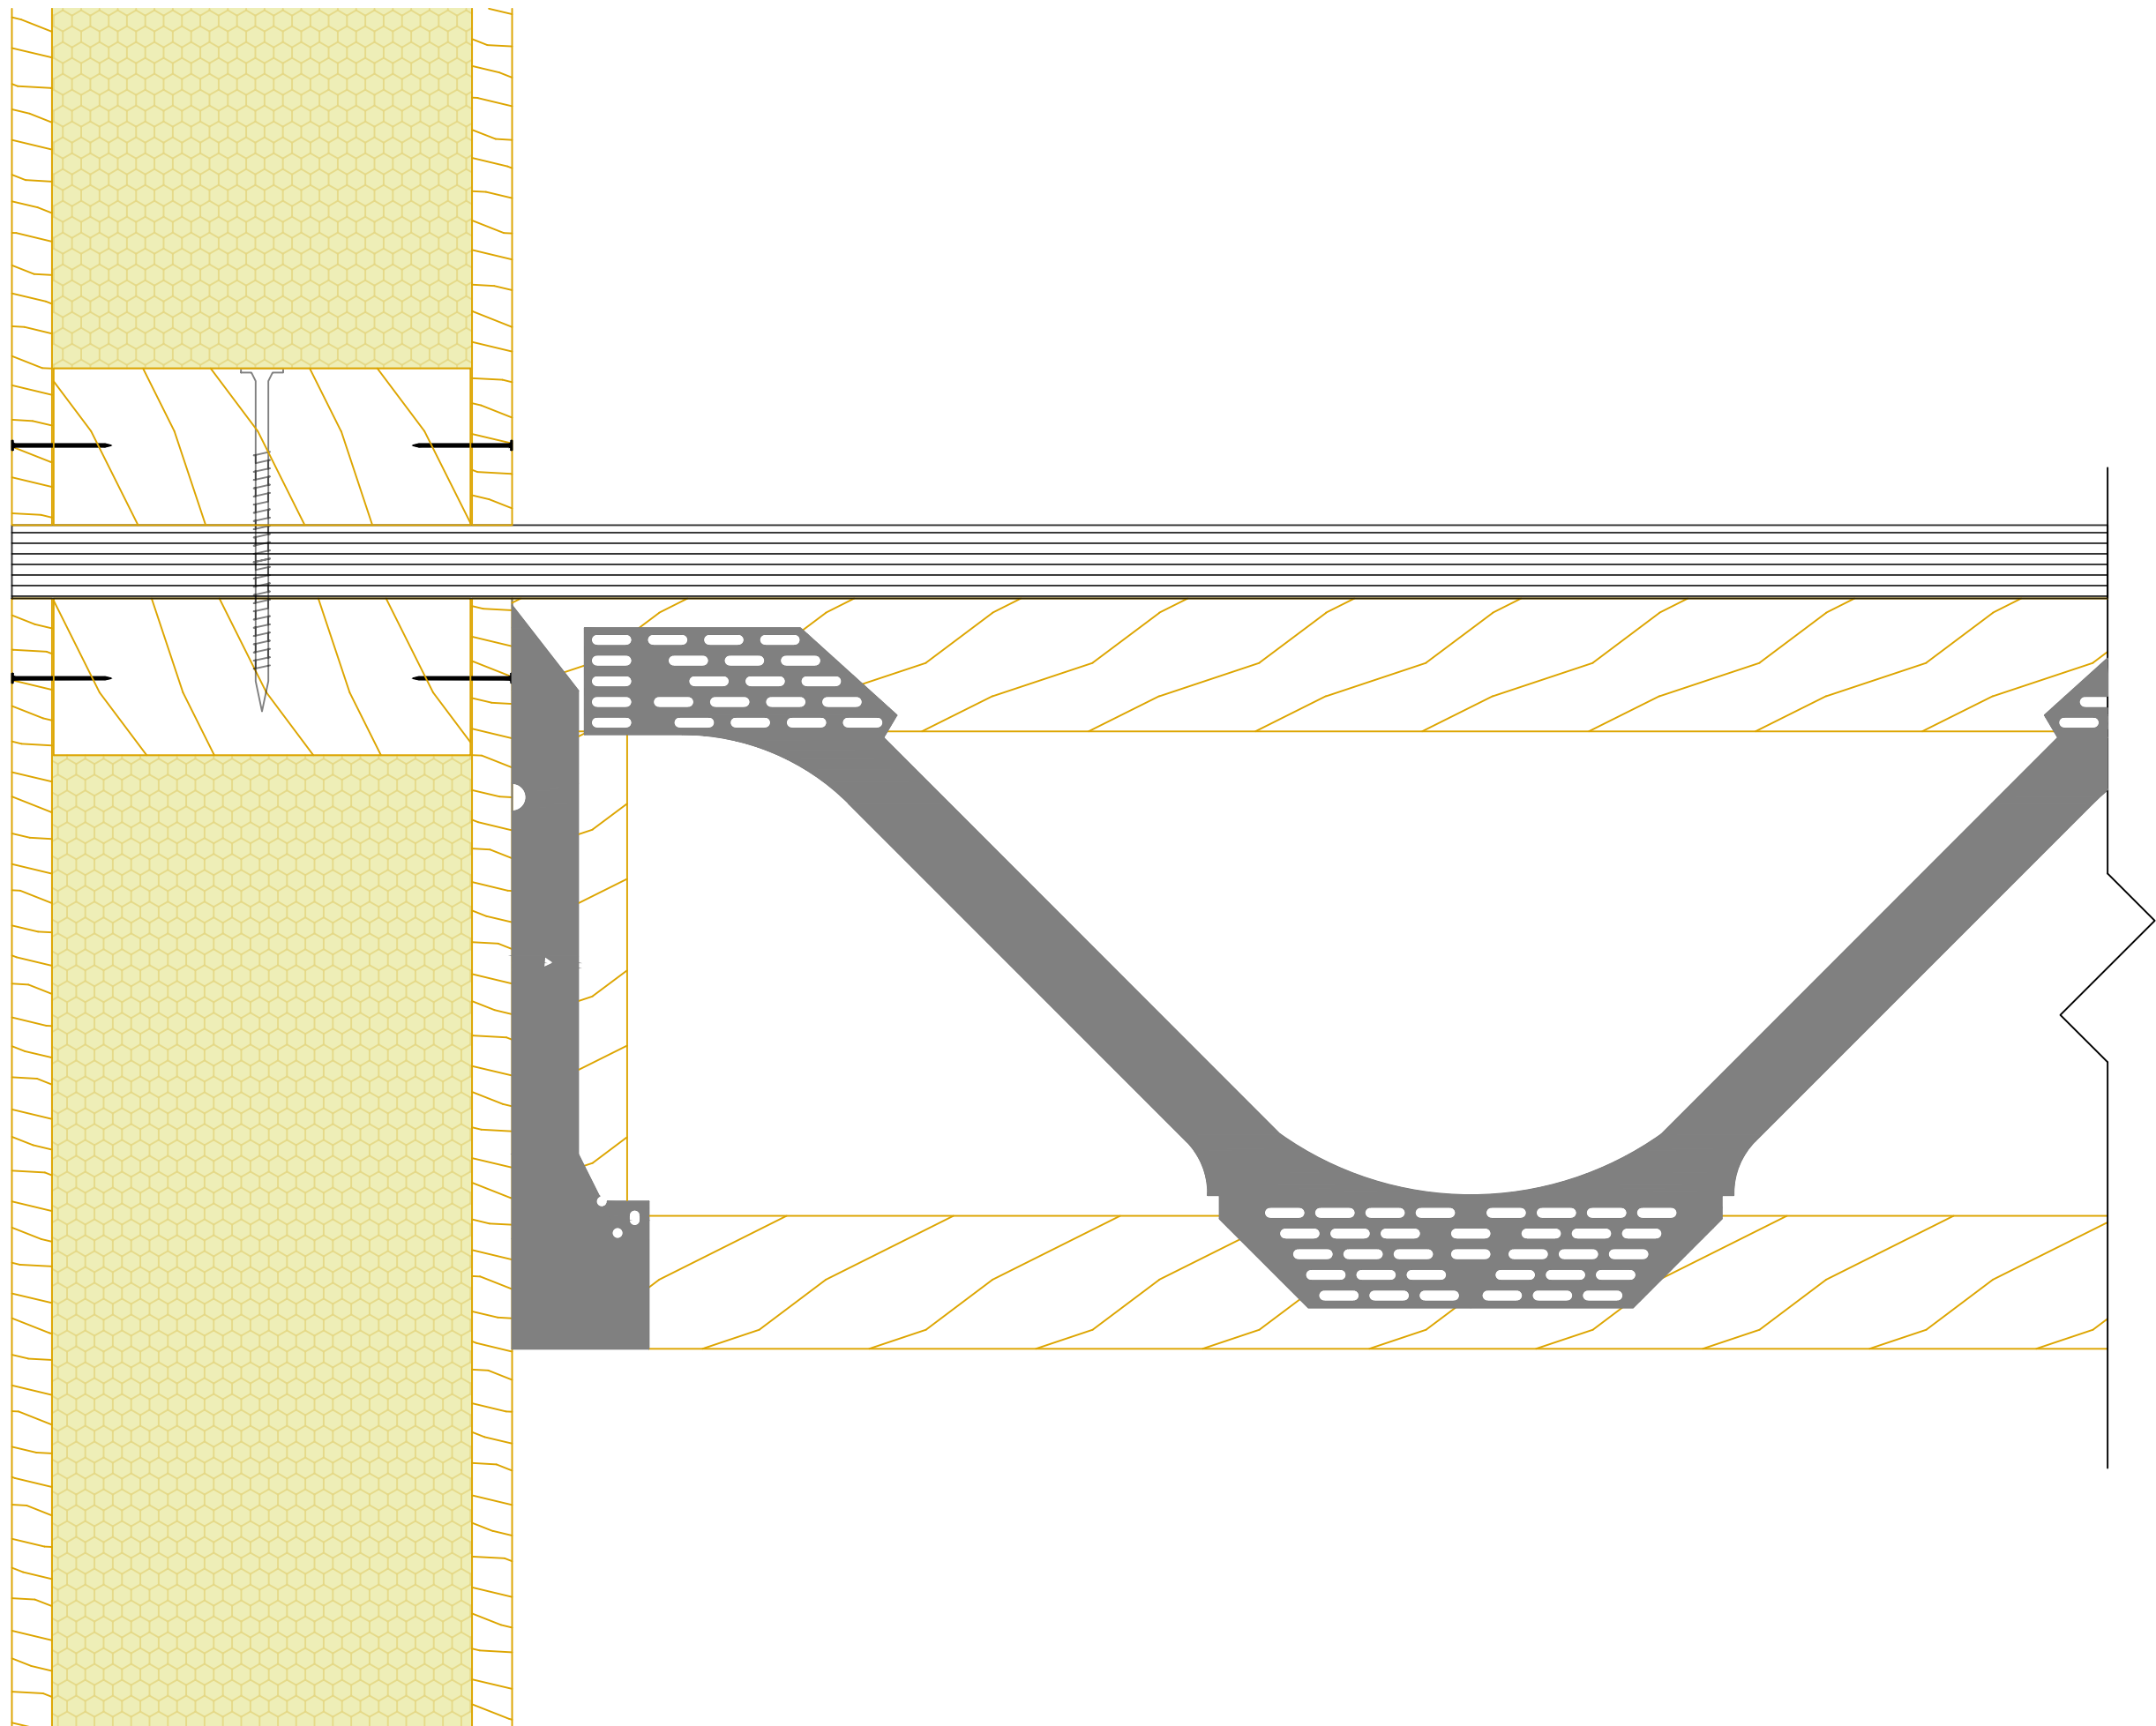

phone: 01590 642 087
e-mail: sales@newforestips.co.uk
web: www.newforestips.co.uk

FLOORING TO WALL CONNECTION


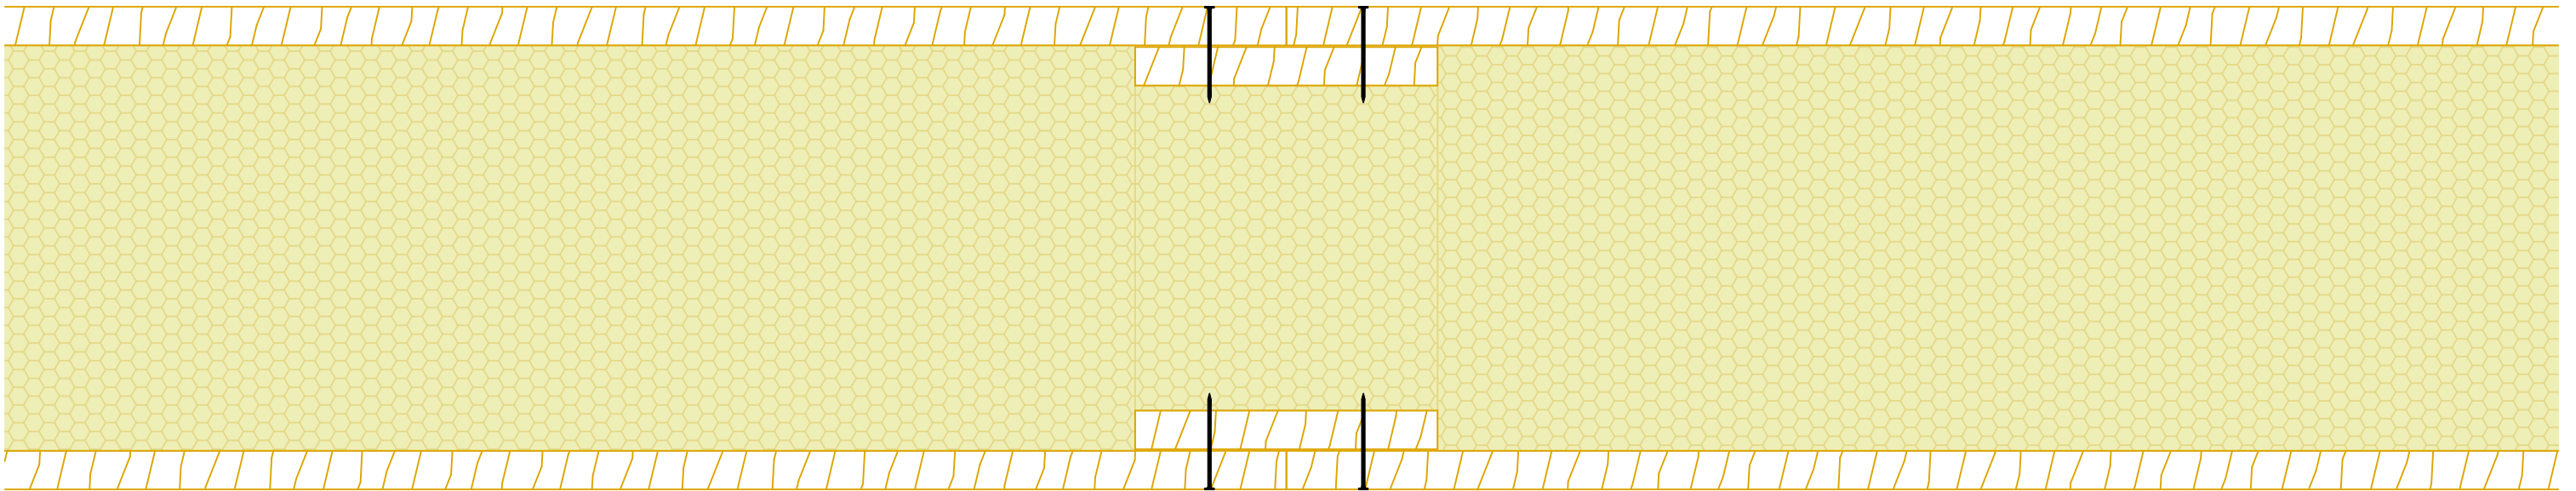
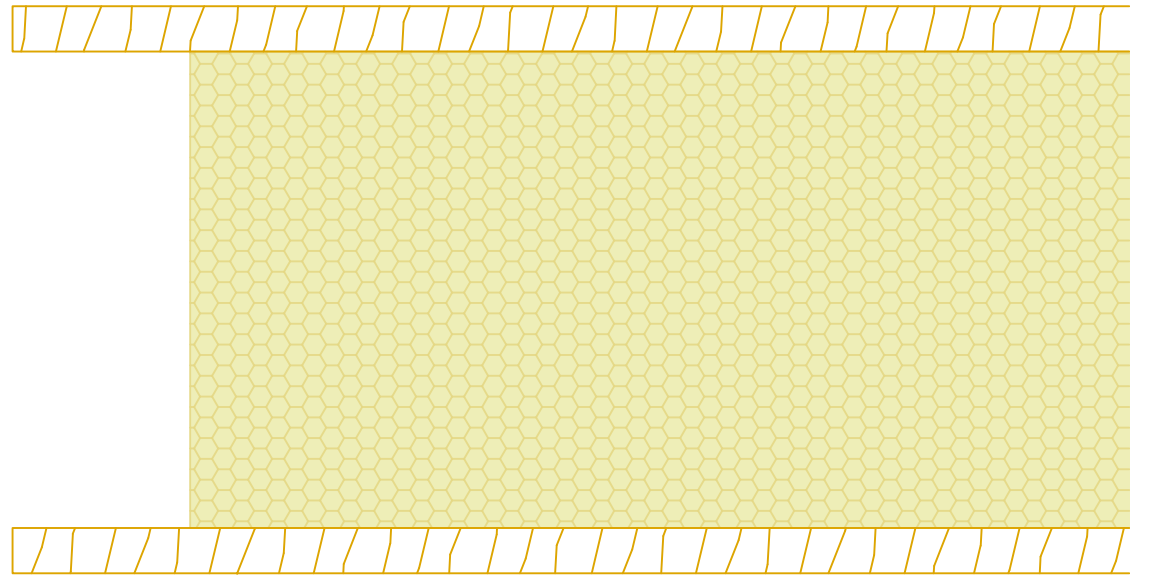
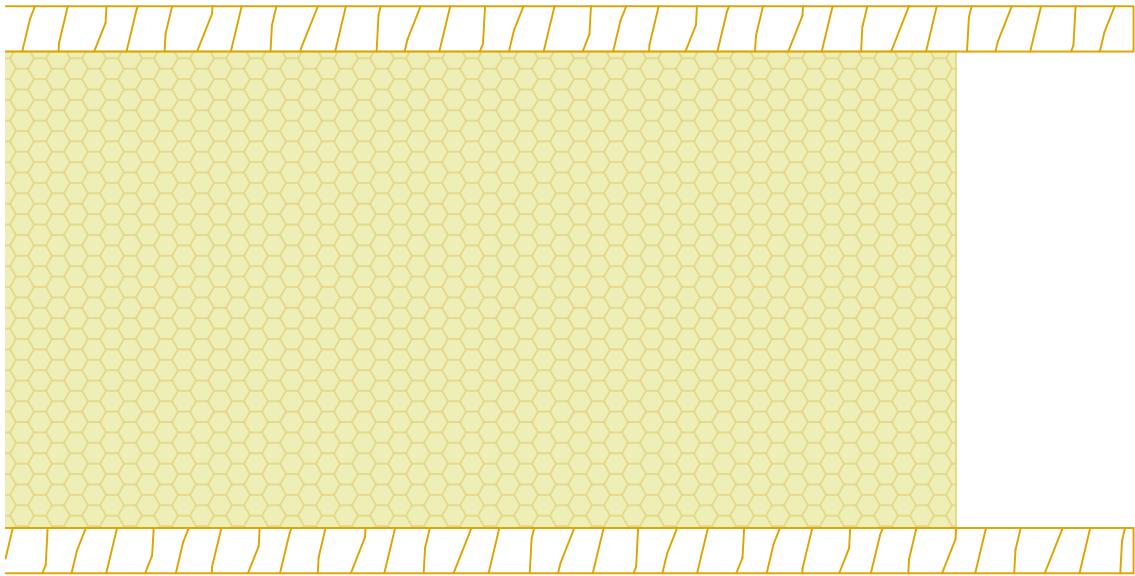


phone: 01590 642 087
e-mail: sales@newforestips.co.uk
web: www.newforestips.co.uk



SIP INSULATED CONNECTION SPLINE DETAIL


*All dimensions shown are in mm, dimensions to be checked on-site prior to manufacture and are subject to change upon site measure.
*This drawing is property of New Forest SIPs Ltd. and may not be reproduced, copied or given to any third parties for any reason whatsoever without written consent from New Forest SIPs Ltd.
*Drawn by: JG

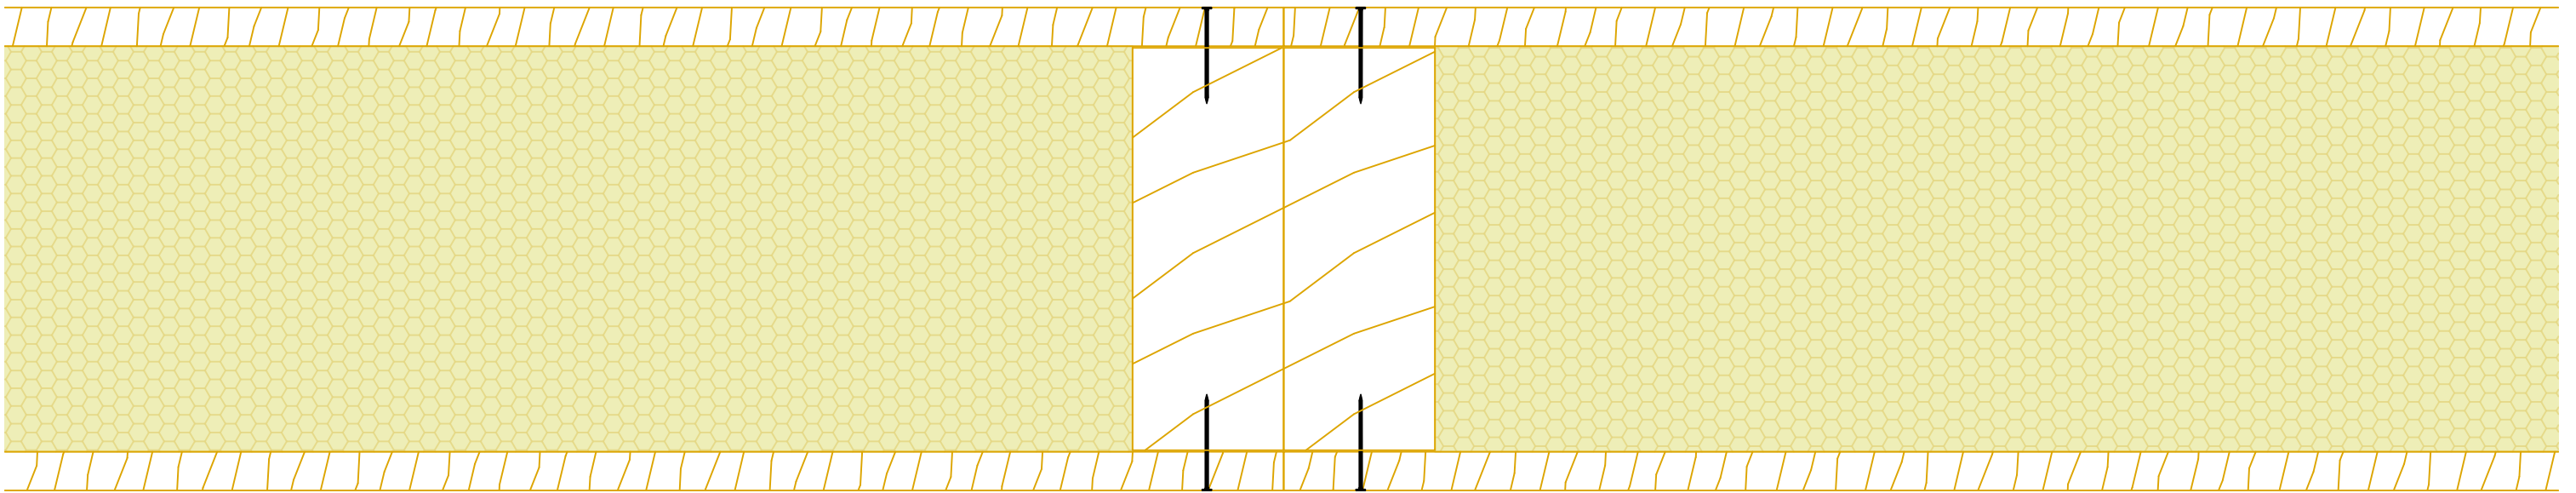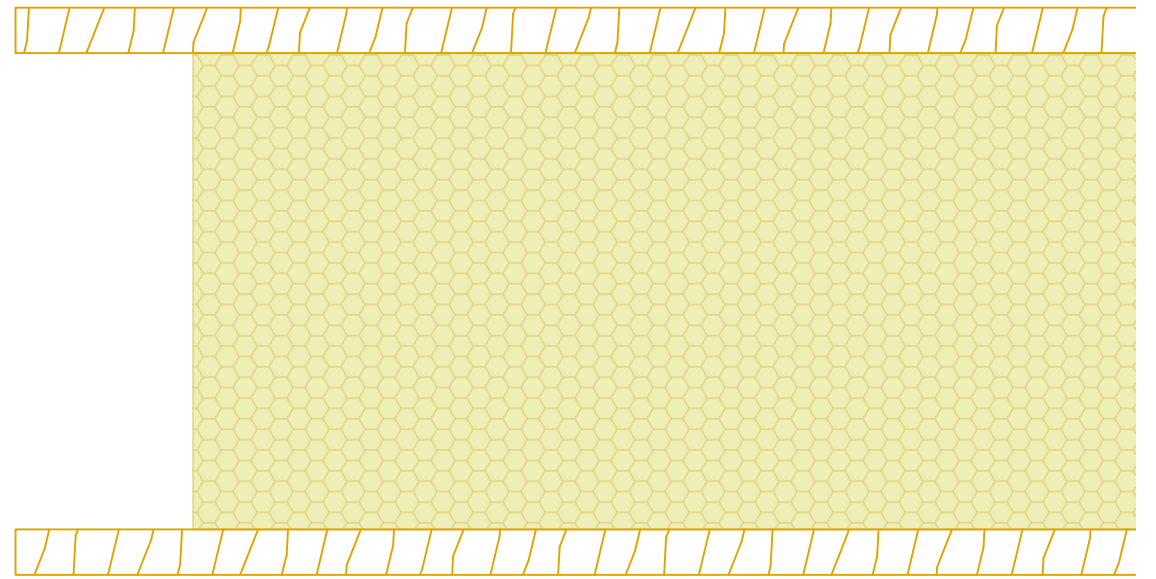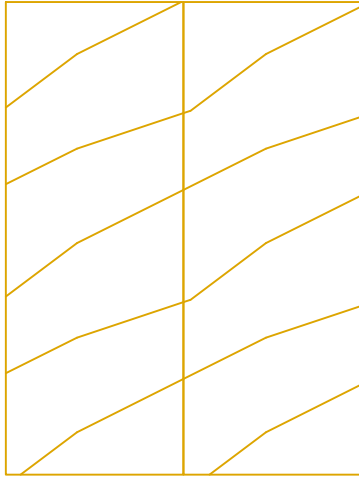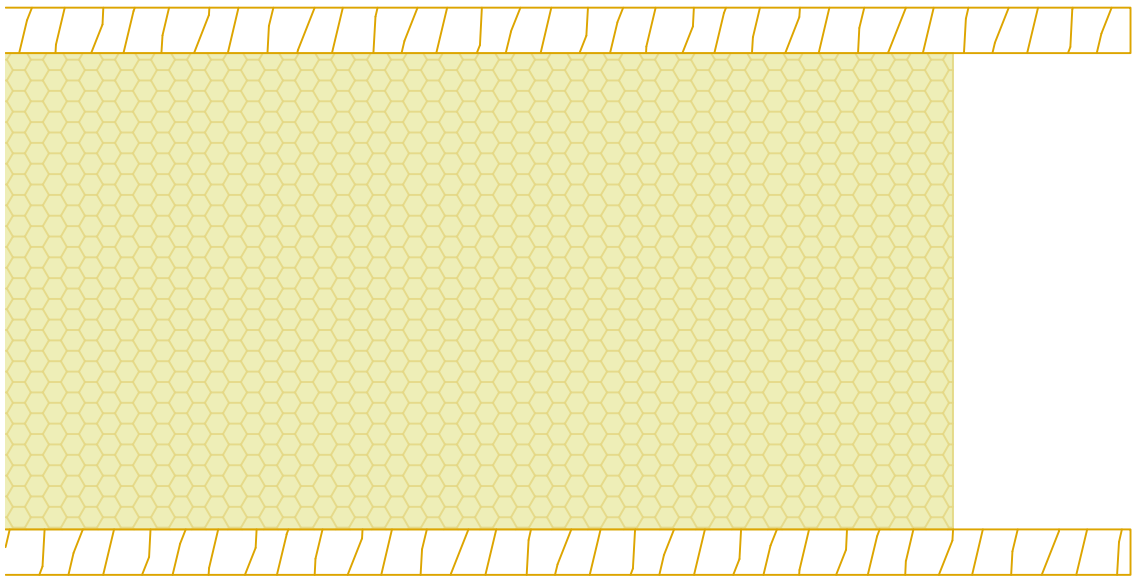

phone: 01590 642 087
e-mail: sales@newforesttips.co.uk
web: www.newforesttips.co.uk

TIMBER CONNECTION SPLINE DETAIL


*All dimensions shown are in mm, dimensions to be checked on-site prior to manufacture and are subject to change upon site measure.
*This drawing is property of New Forest SIPs Ltd. and may not be reproduced, copied or given to any third parties for any reason whatsoever without written consent from New Forest SIPs Ltd.
*Drawn by: JG

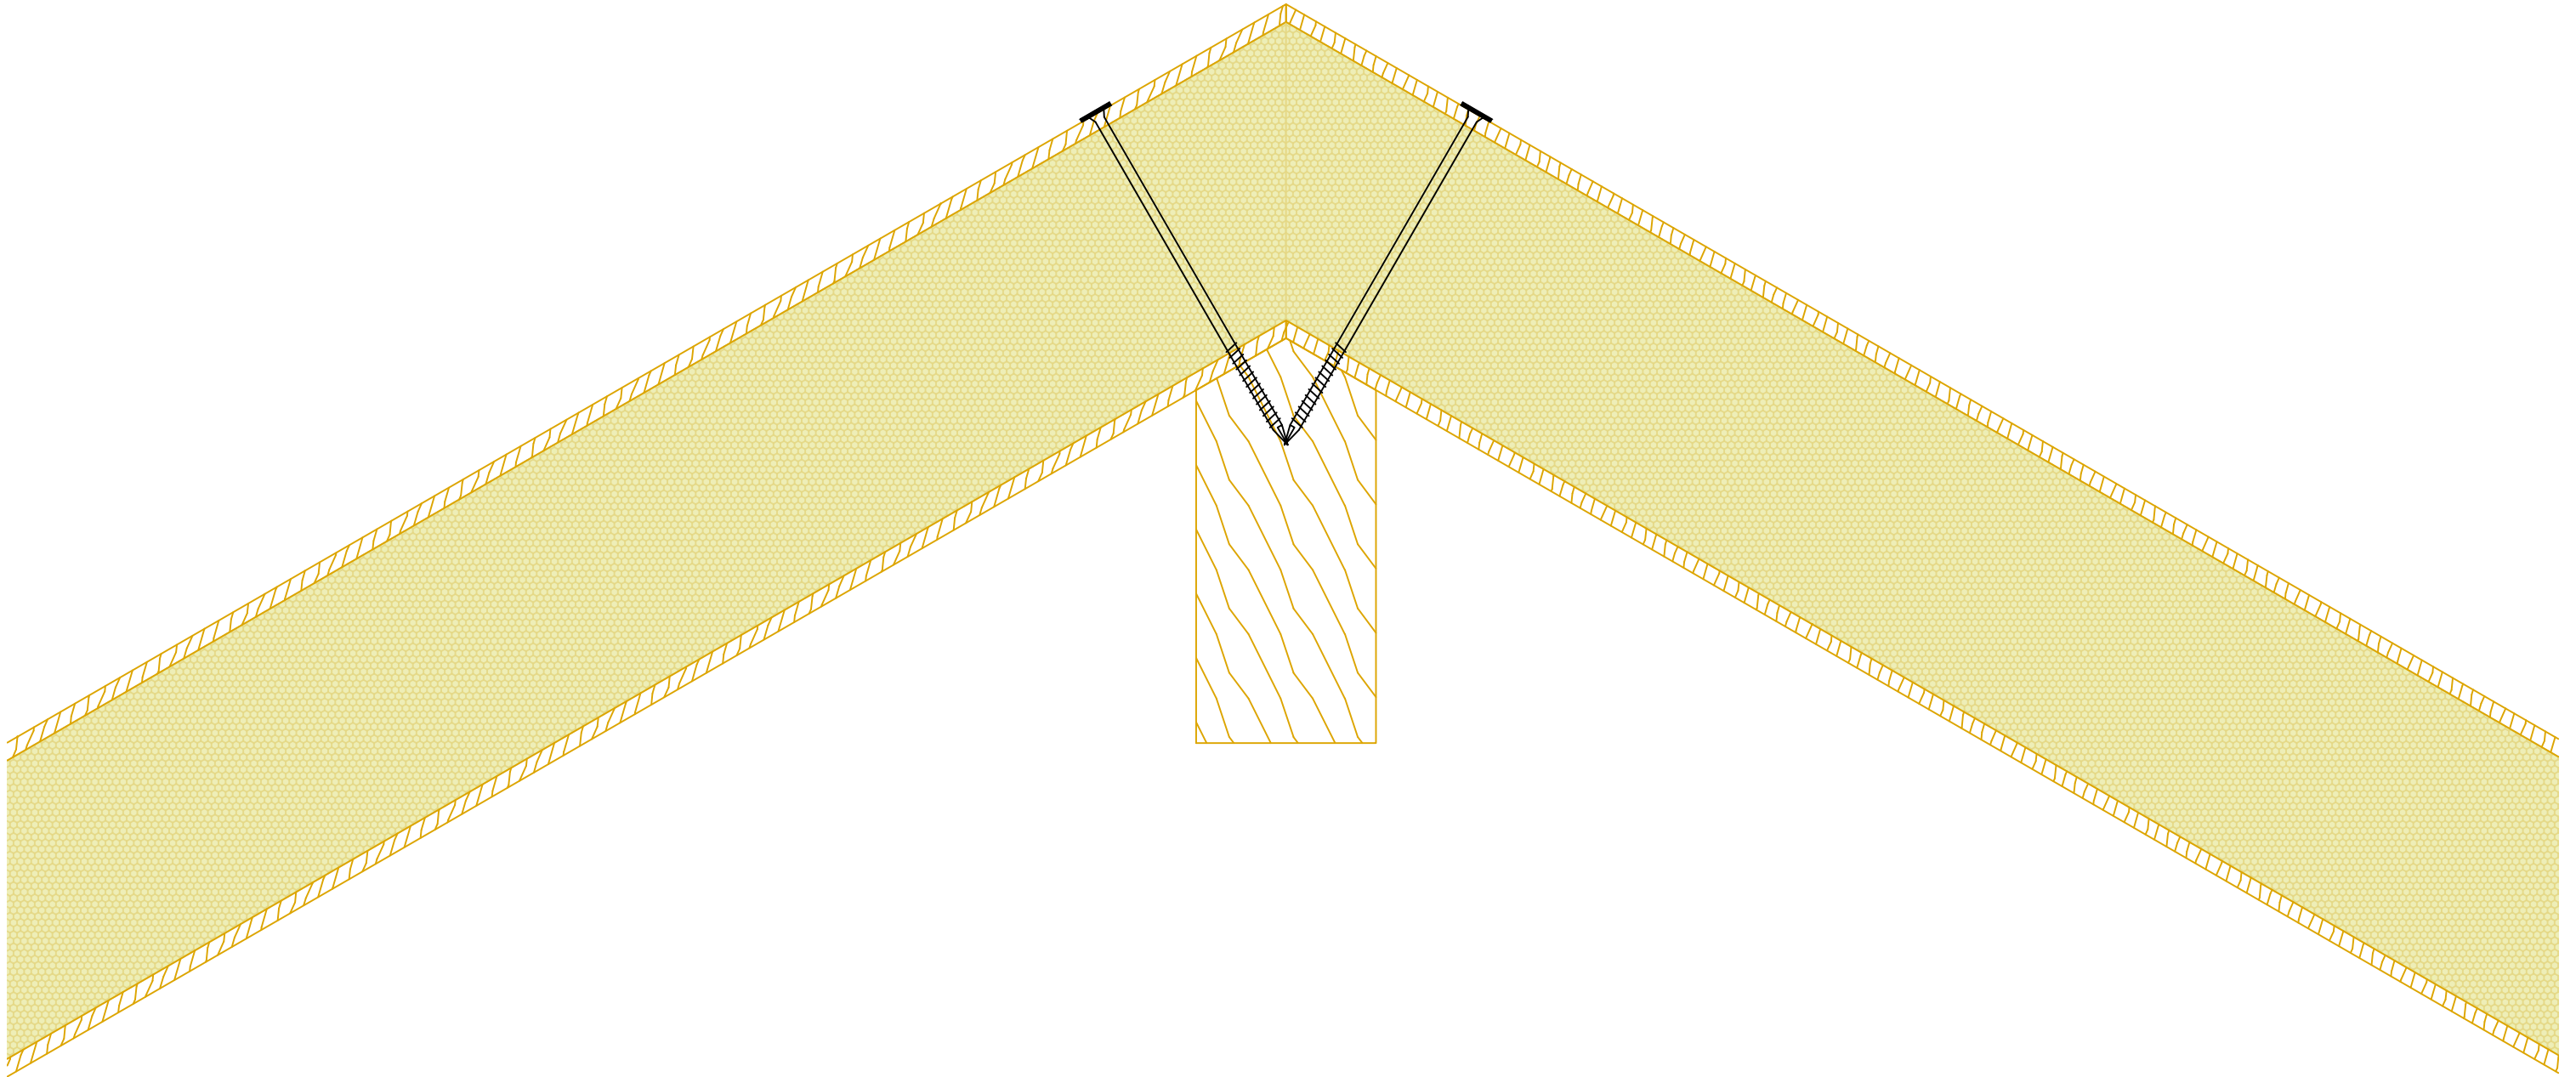

phone: 01590 642 087
e-mail: sales@newforesttips.co.uk
web: www.newforesttips.co.uk


GLULAM RIDGE DETAIL

*All dimensions shown are in mm, dimensions to be checked on-site prior to manufacture and are subject to change upon site measure.
*This drawing is property of New Forest SIPs Ltd. and may not be reproduced, copied or given to any third parties for any reason whatsoever without written consent from New Forest SIPs Ltd.
*Drawn by: JG

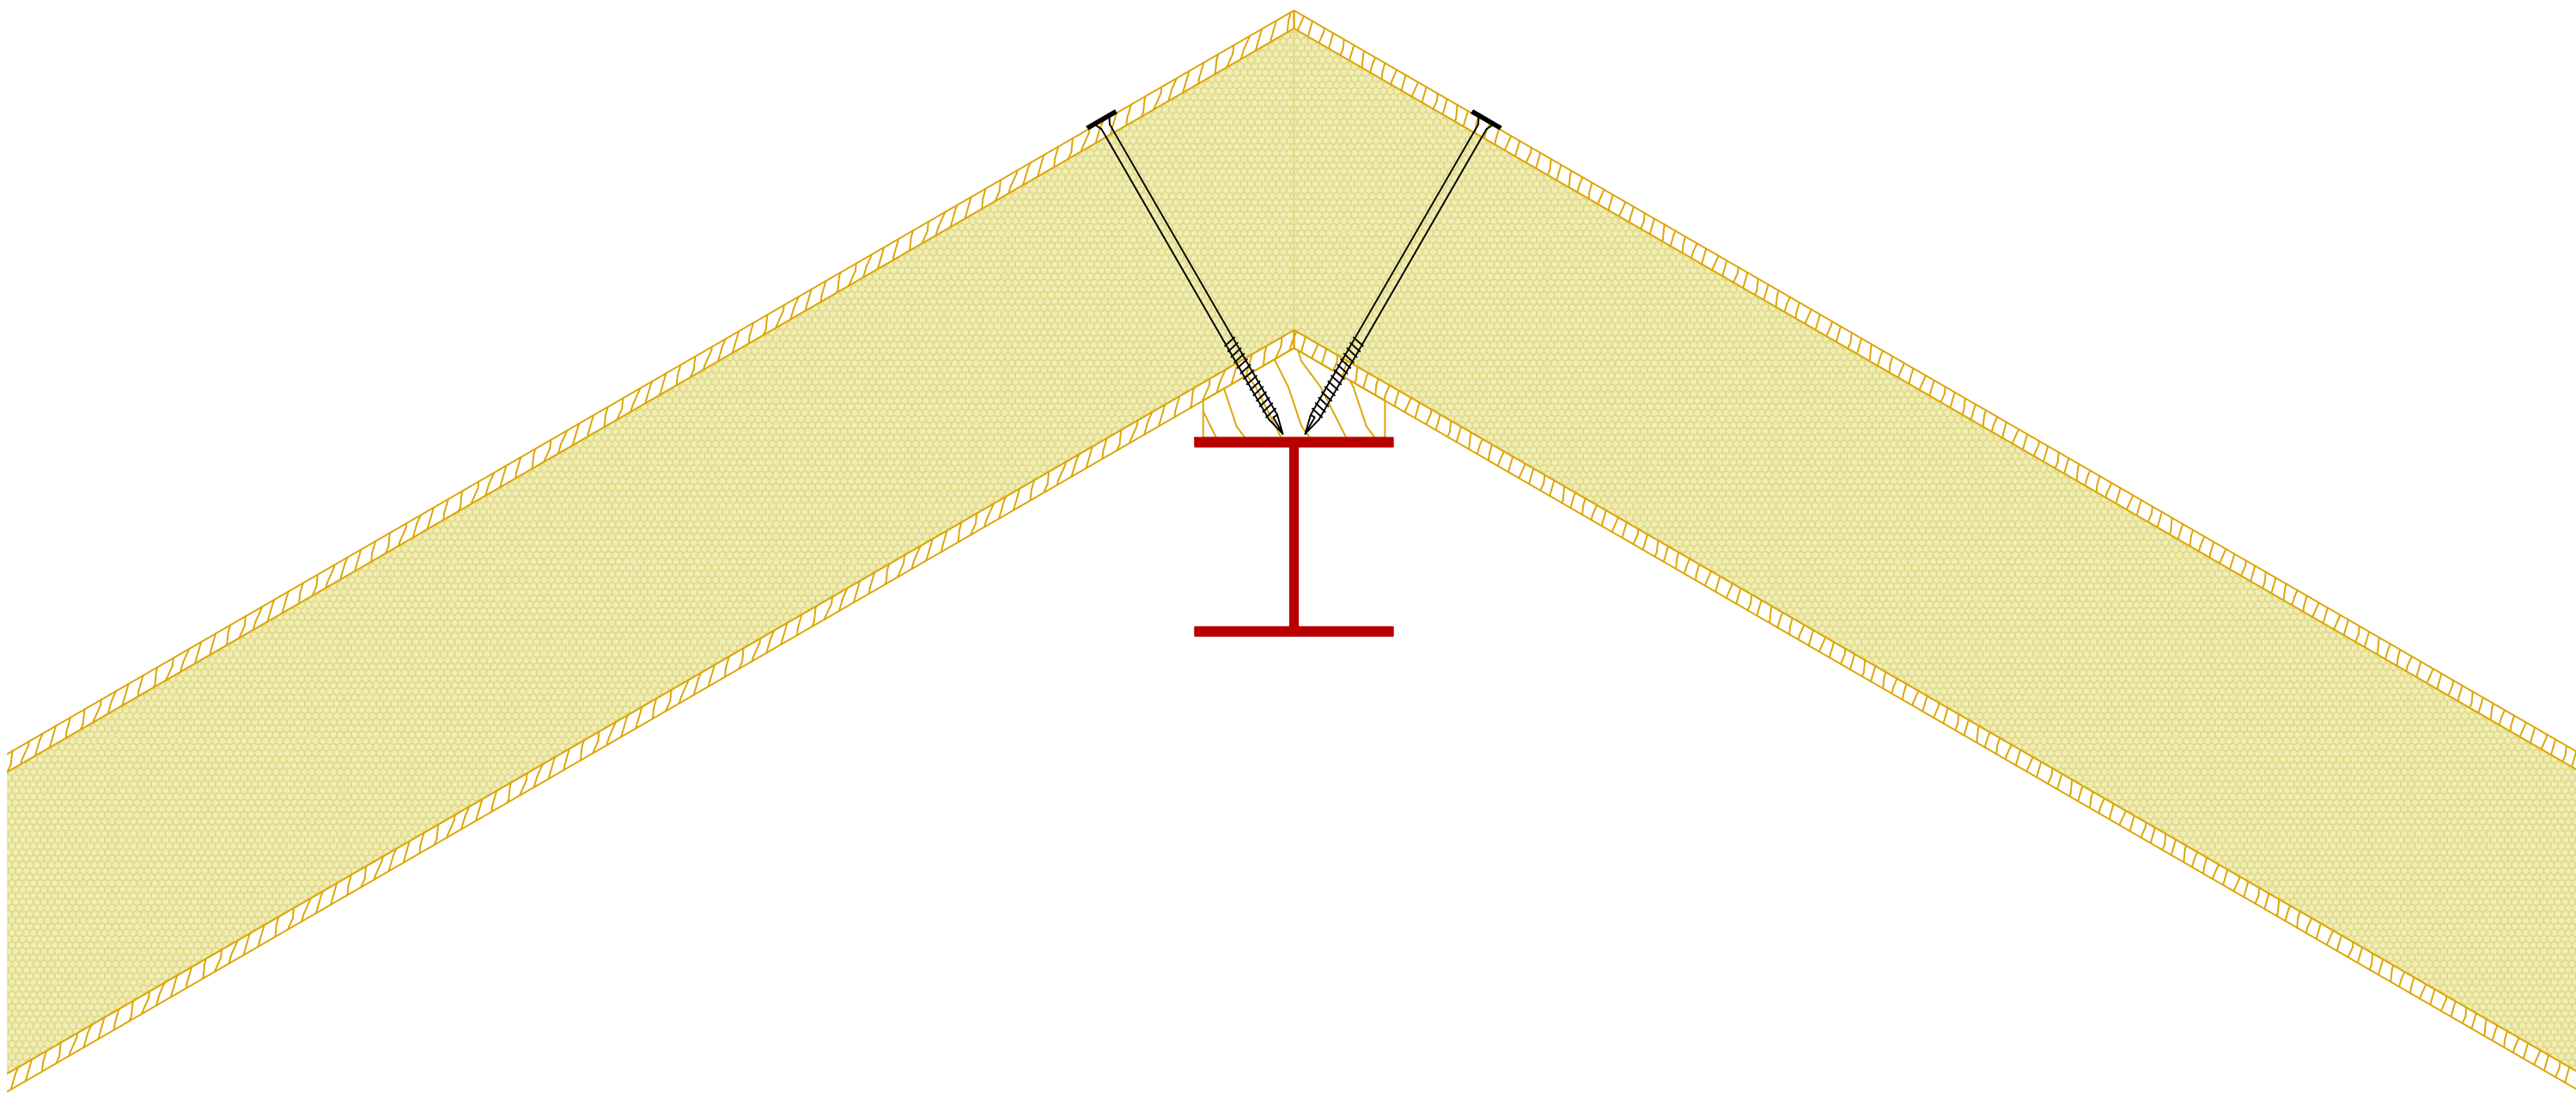


phone: 01590 642 087
e-mail: sales@newforesttips.co.uk
web: www.newforesttips.co.uk

GLULAM RIDGE DETAIL

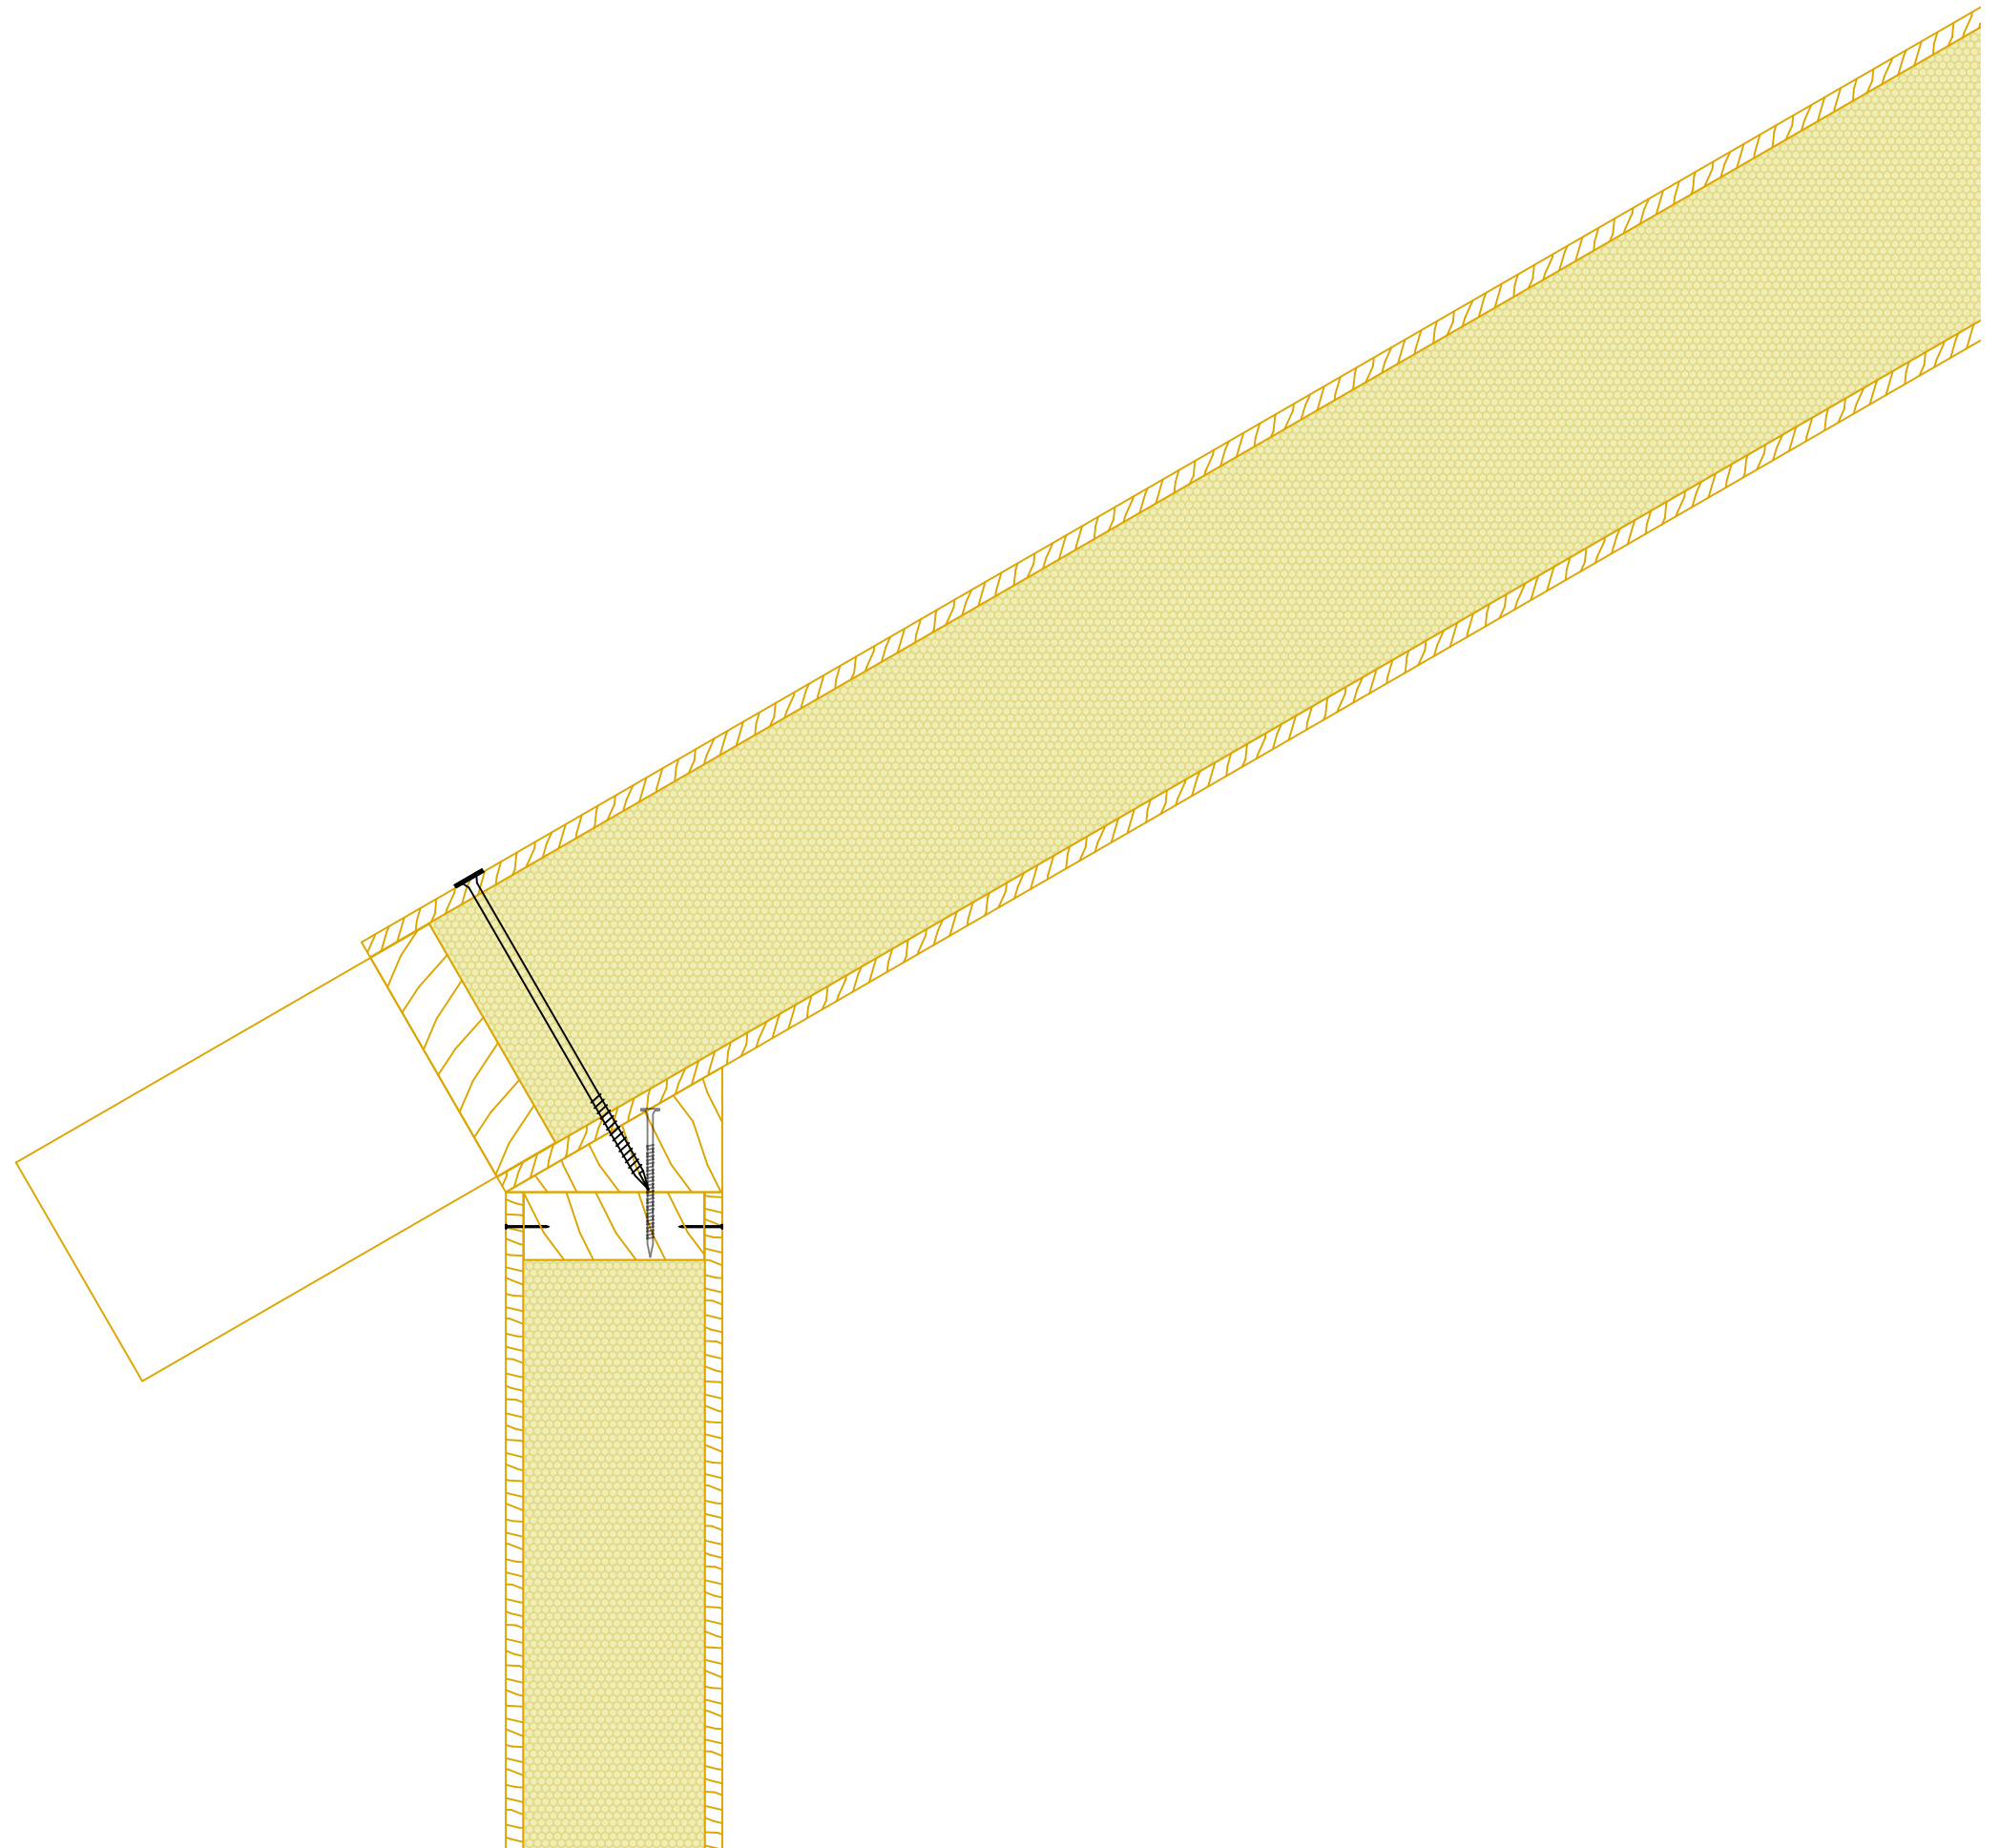

phone: 01590 642 087
e-mail: sales@newforesttips.co.uk
web: www.newforesttips.co.uk

WALL TO PITCHED ROOF SECTION

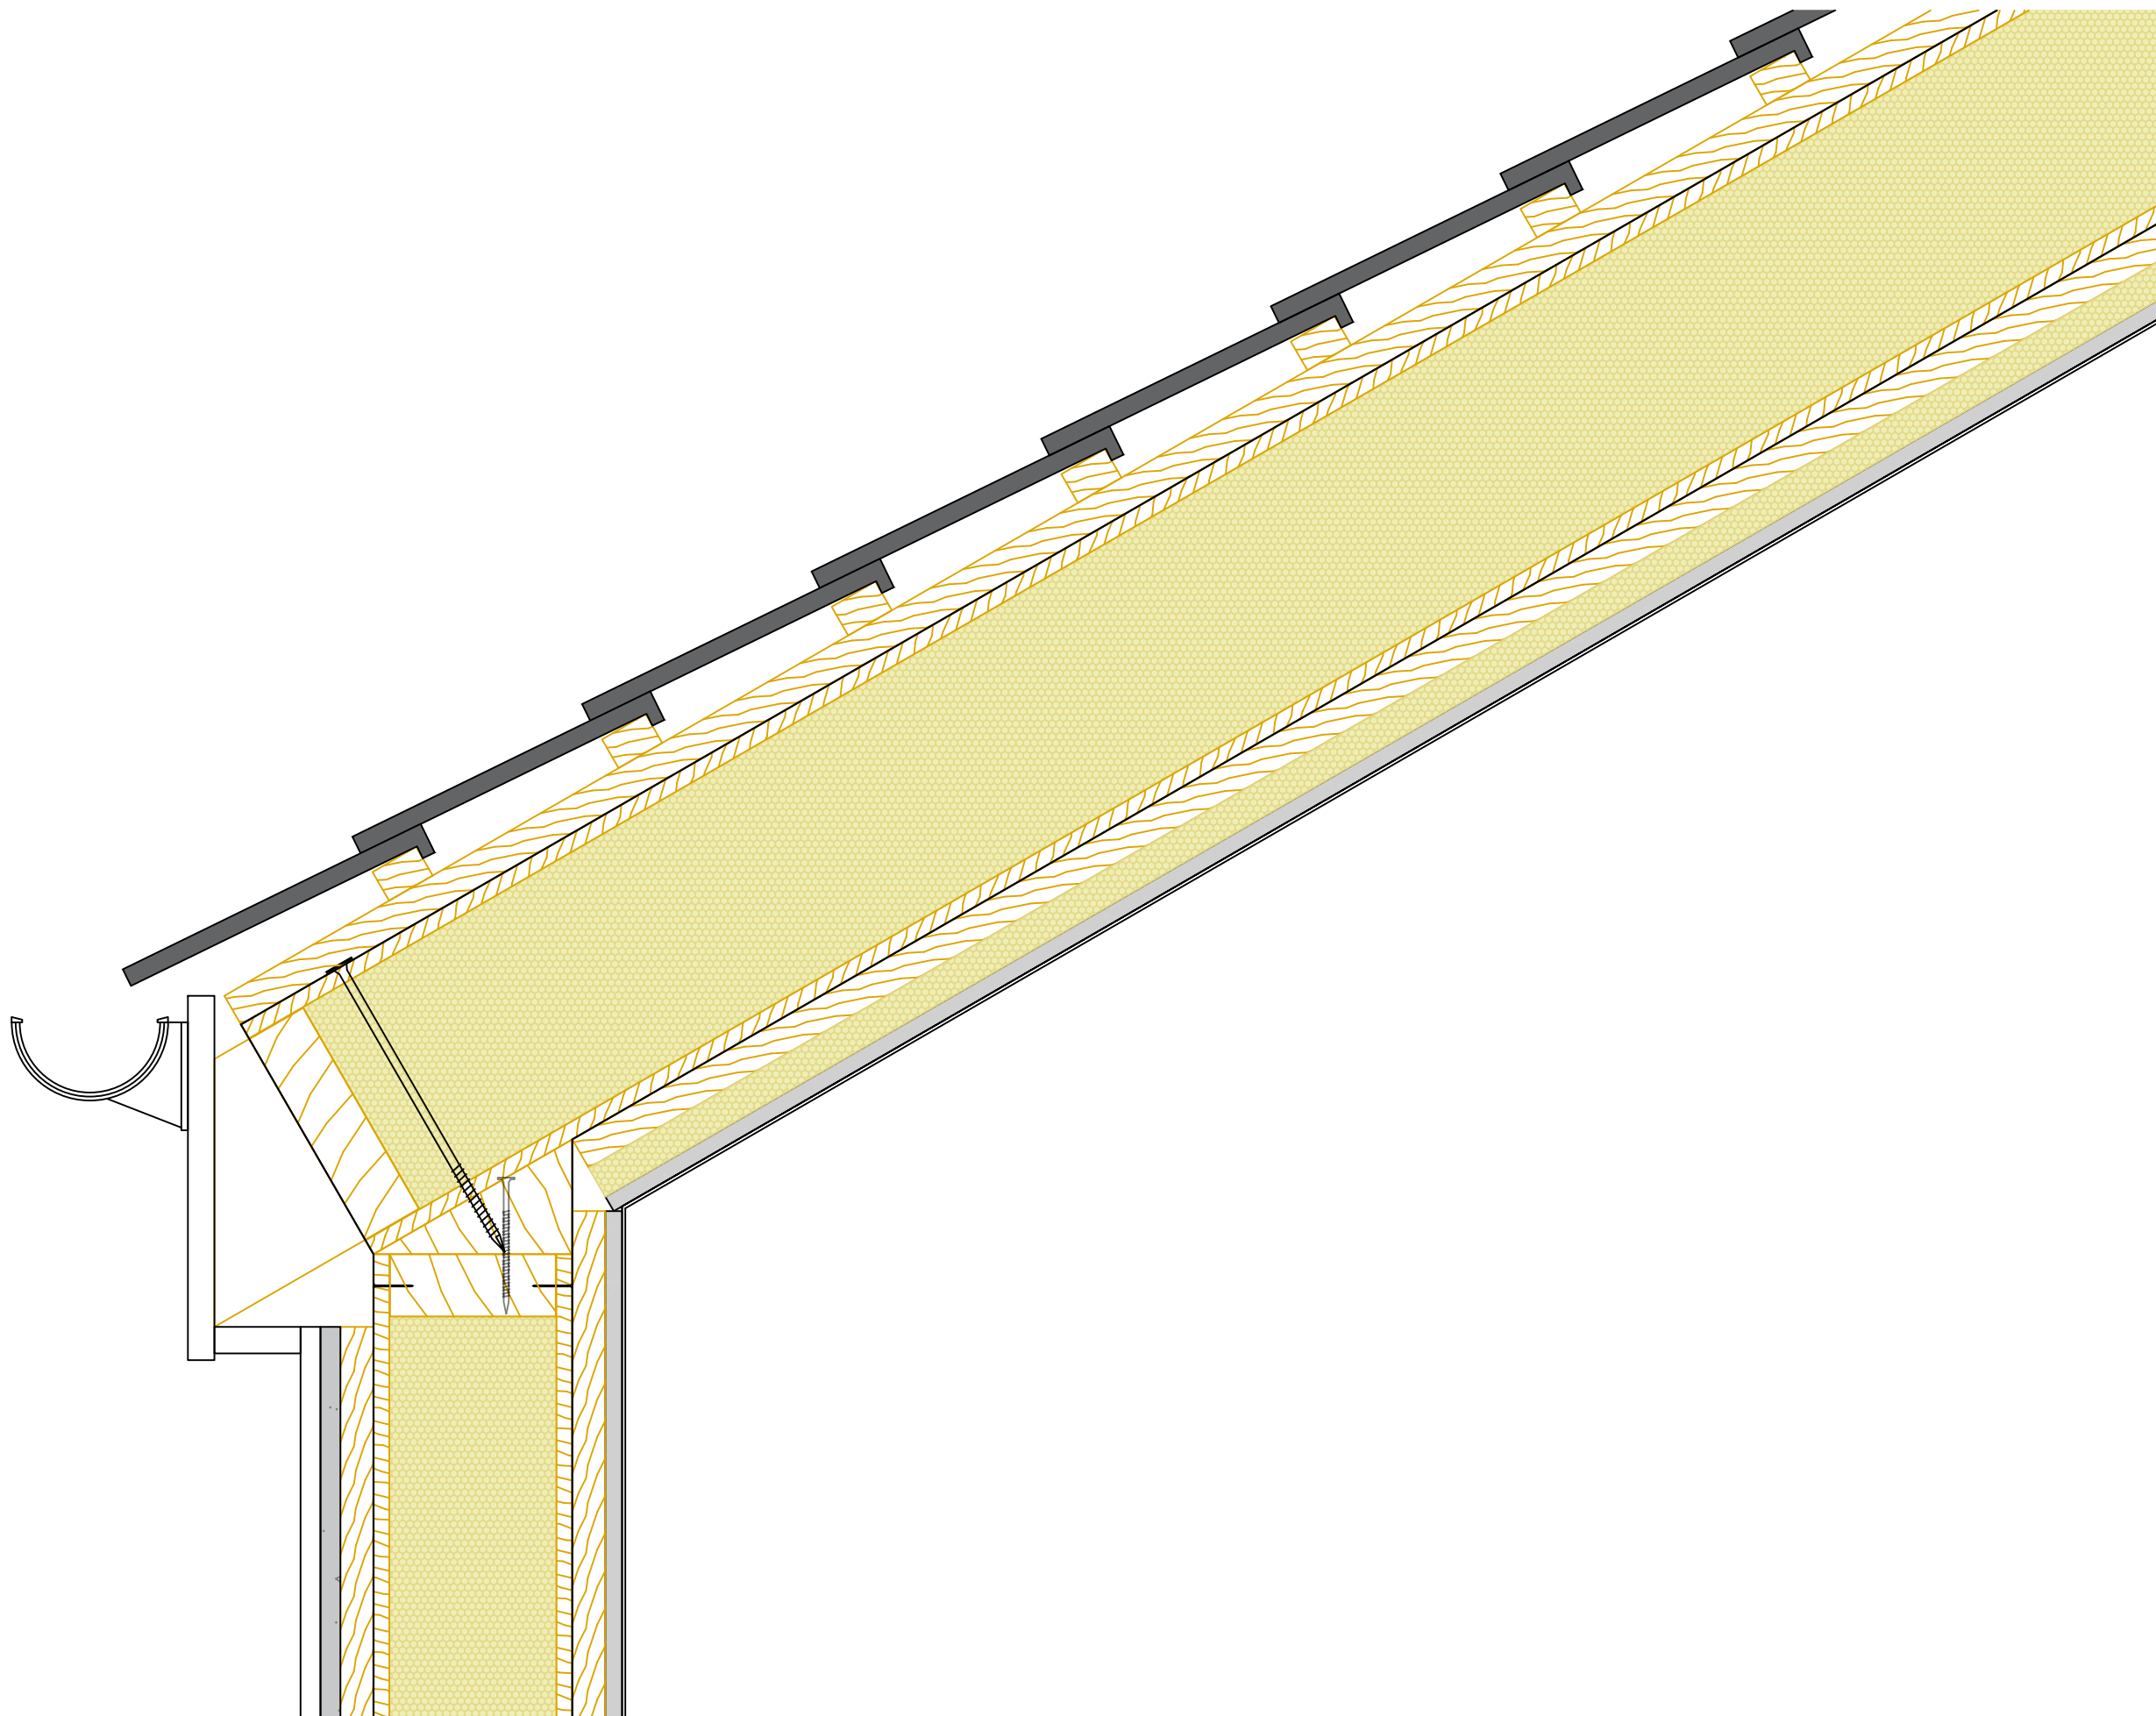


phone: 01590 642 087
e-mail: sales@newforestips.co.uk
web: www.newforestips.co.uk

WALL TO PITCHED ROOF SECTION FINISHED




WALL TO FLAT ROOF SECTION

phone: 01590 642 087
e-mail: sales@newforesttips.co.uk
web: www.newforesttips.co.uk

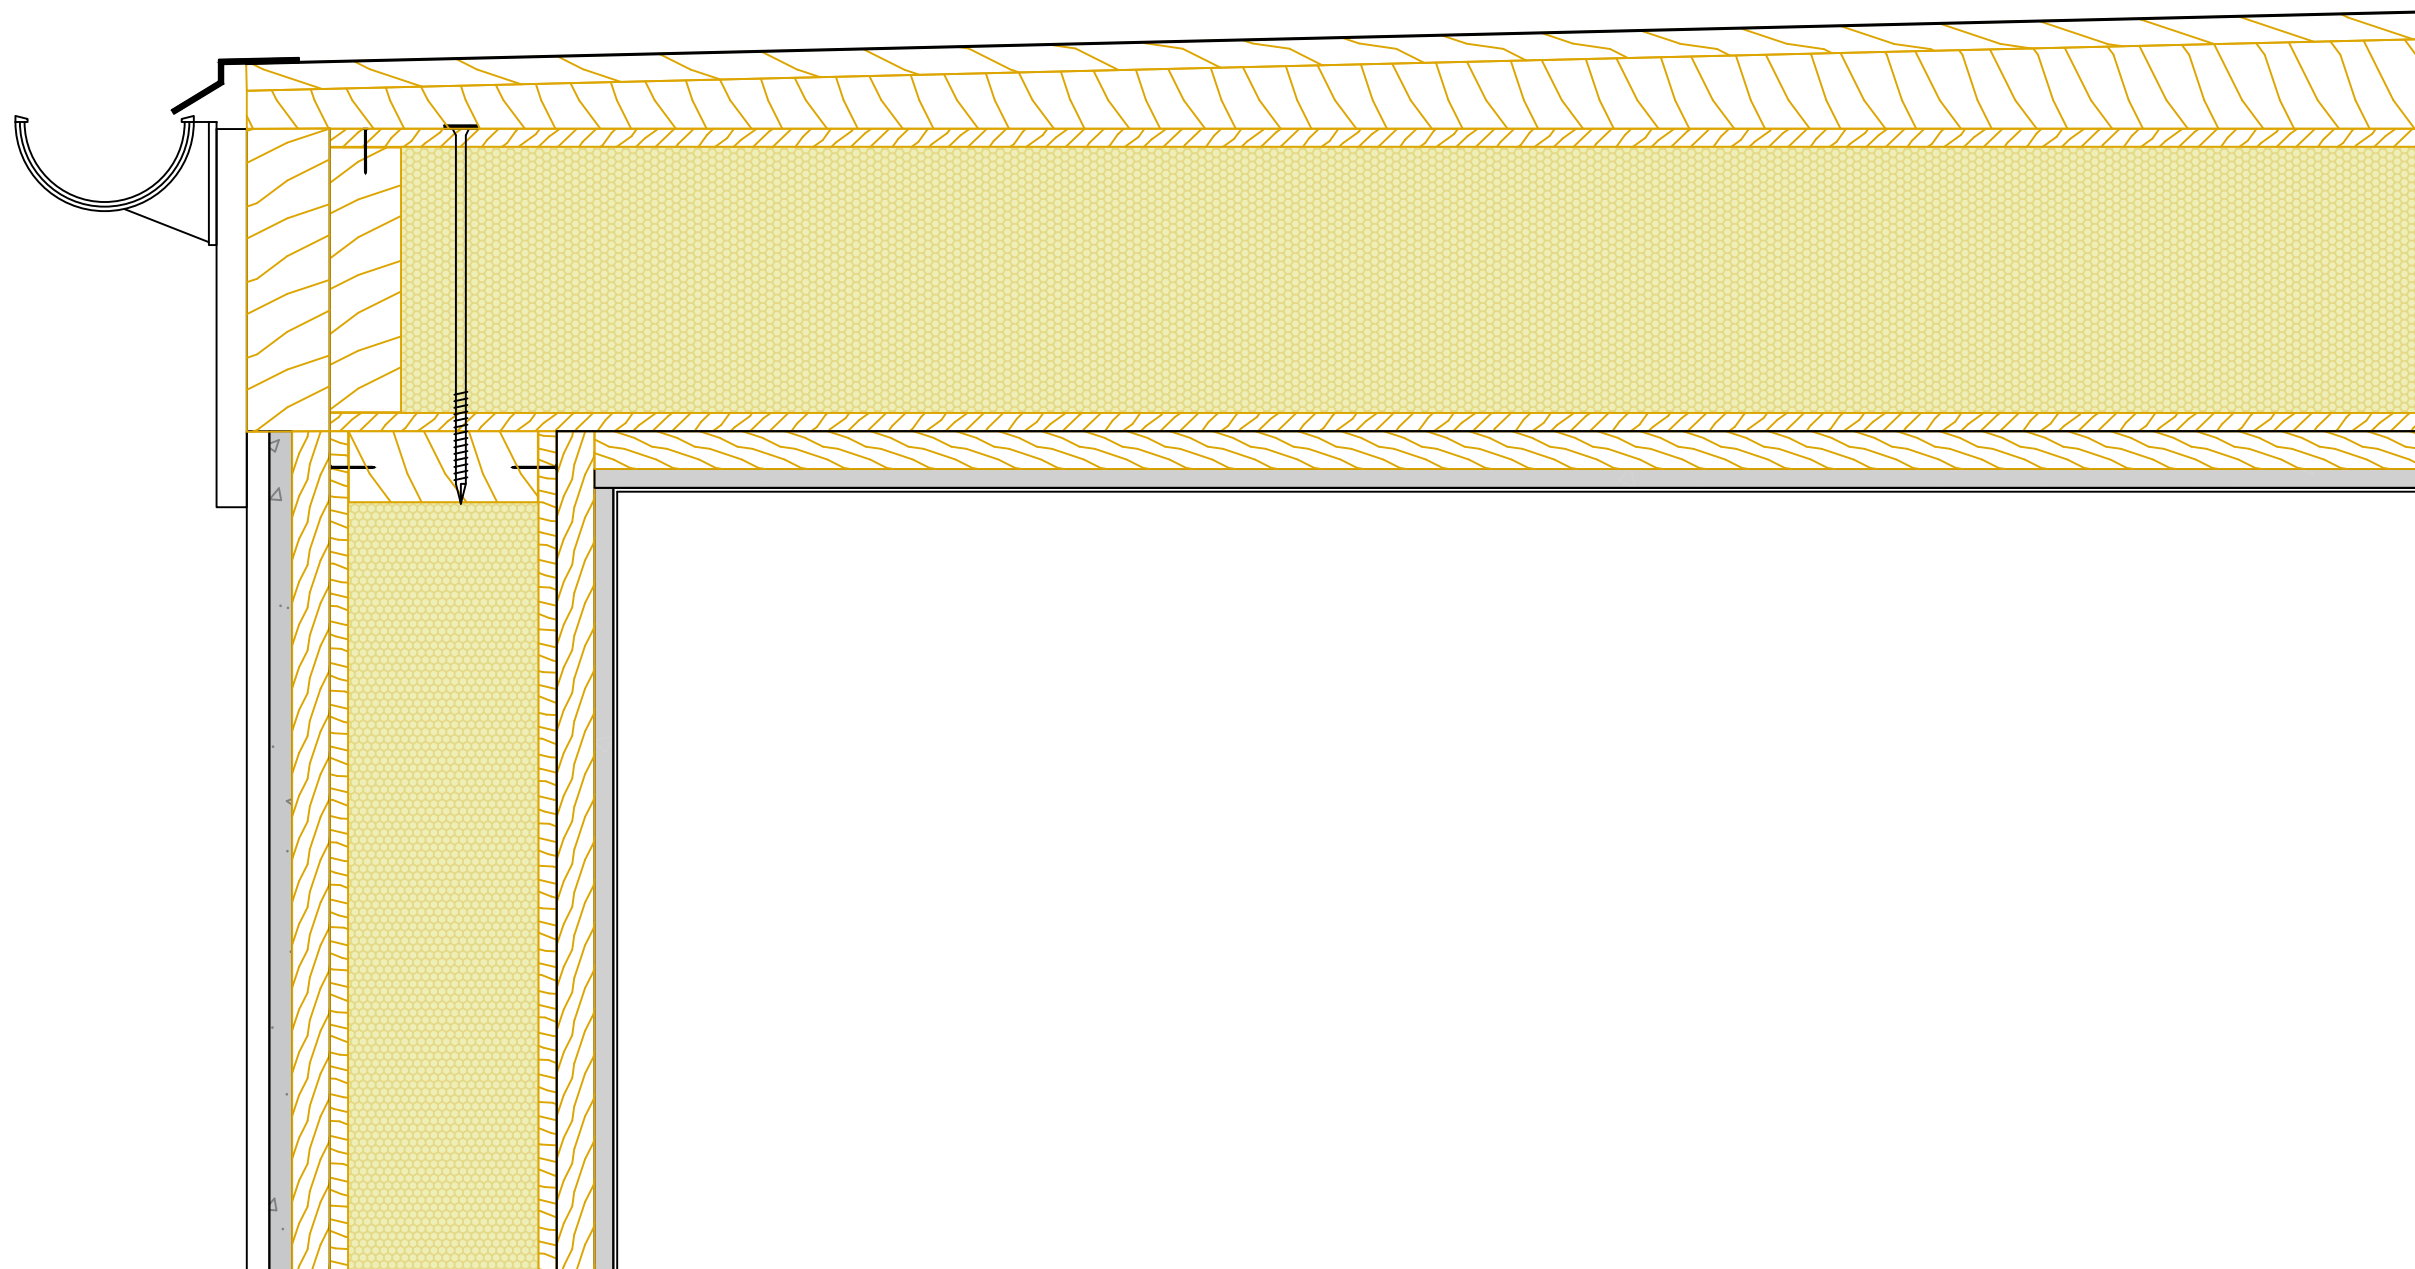

phone: 01590 642 087
e-mail: sales@newforestips.co.uk
web: www.newforestips.co.uk

WALL TO FLAT ROOF SECTION FINISHED

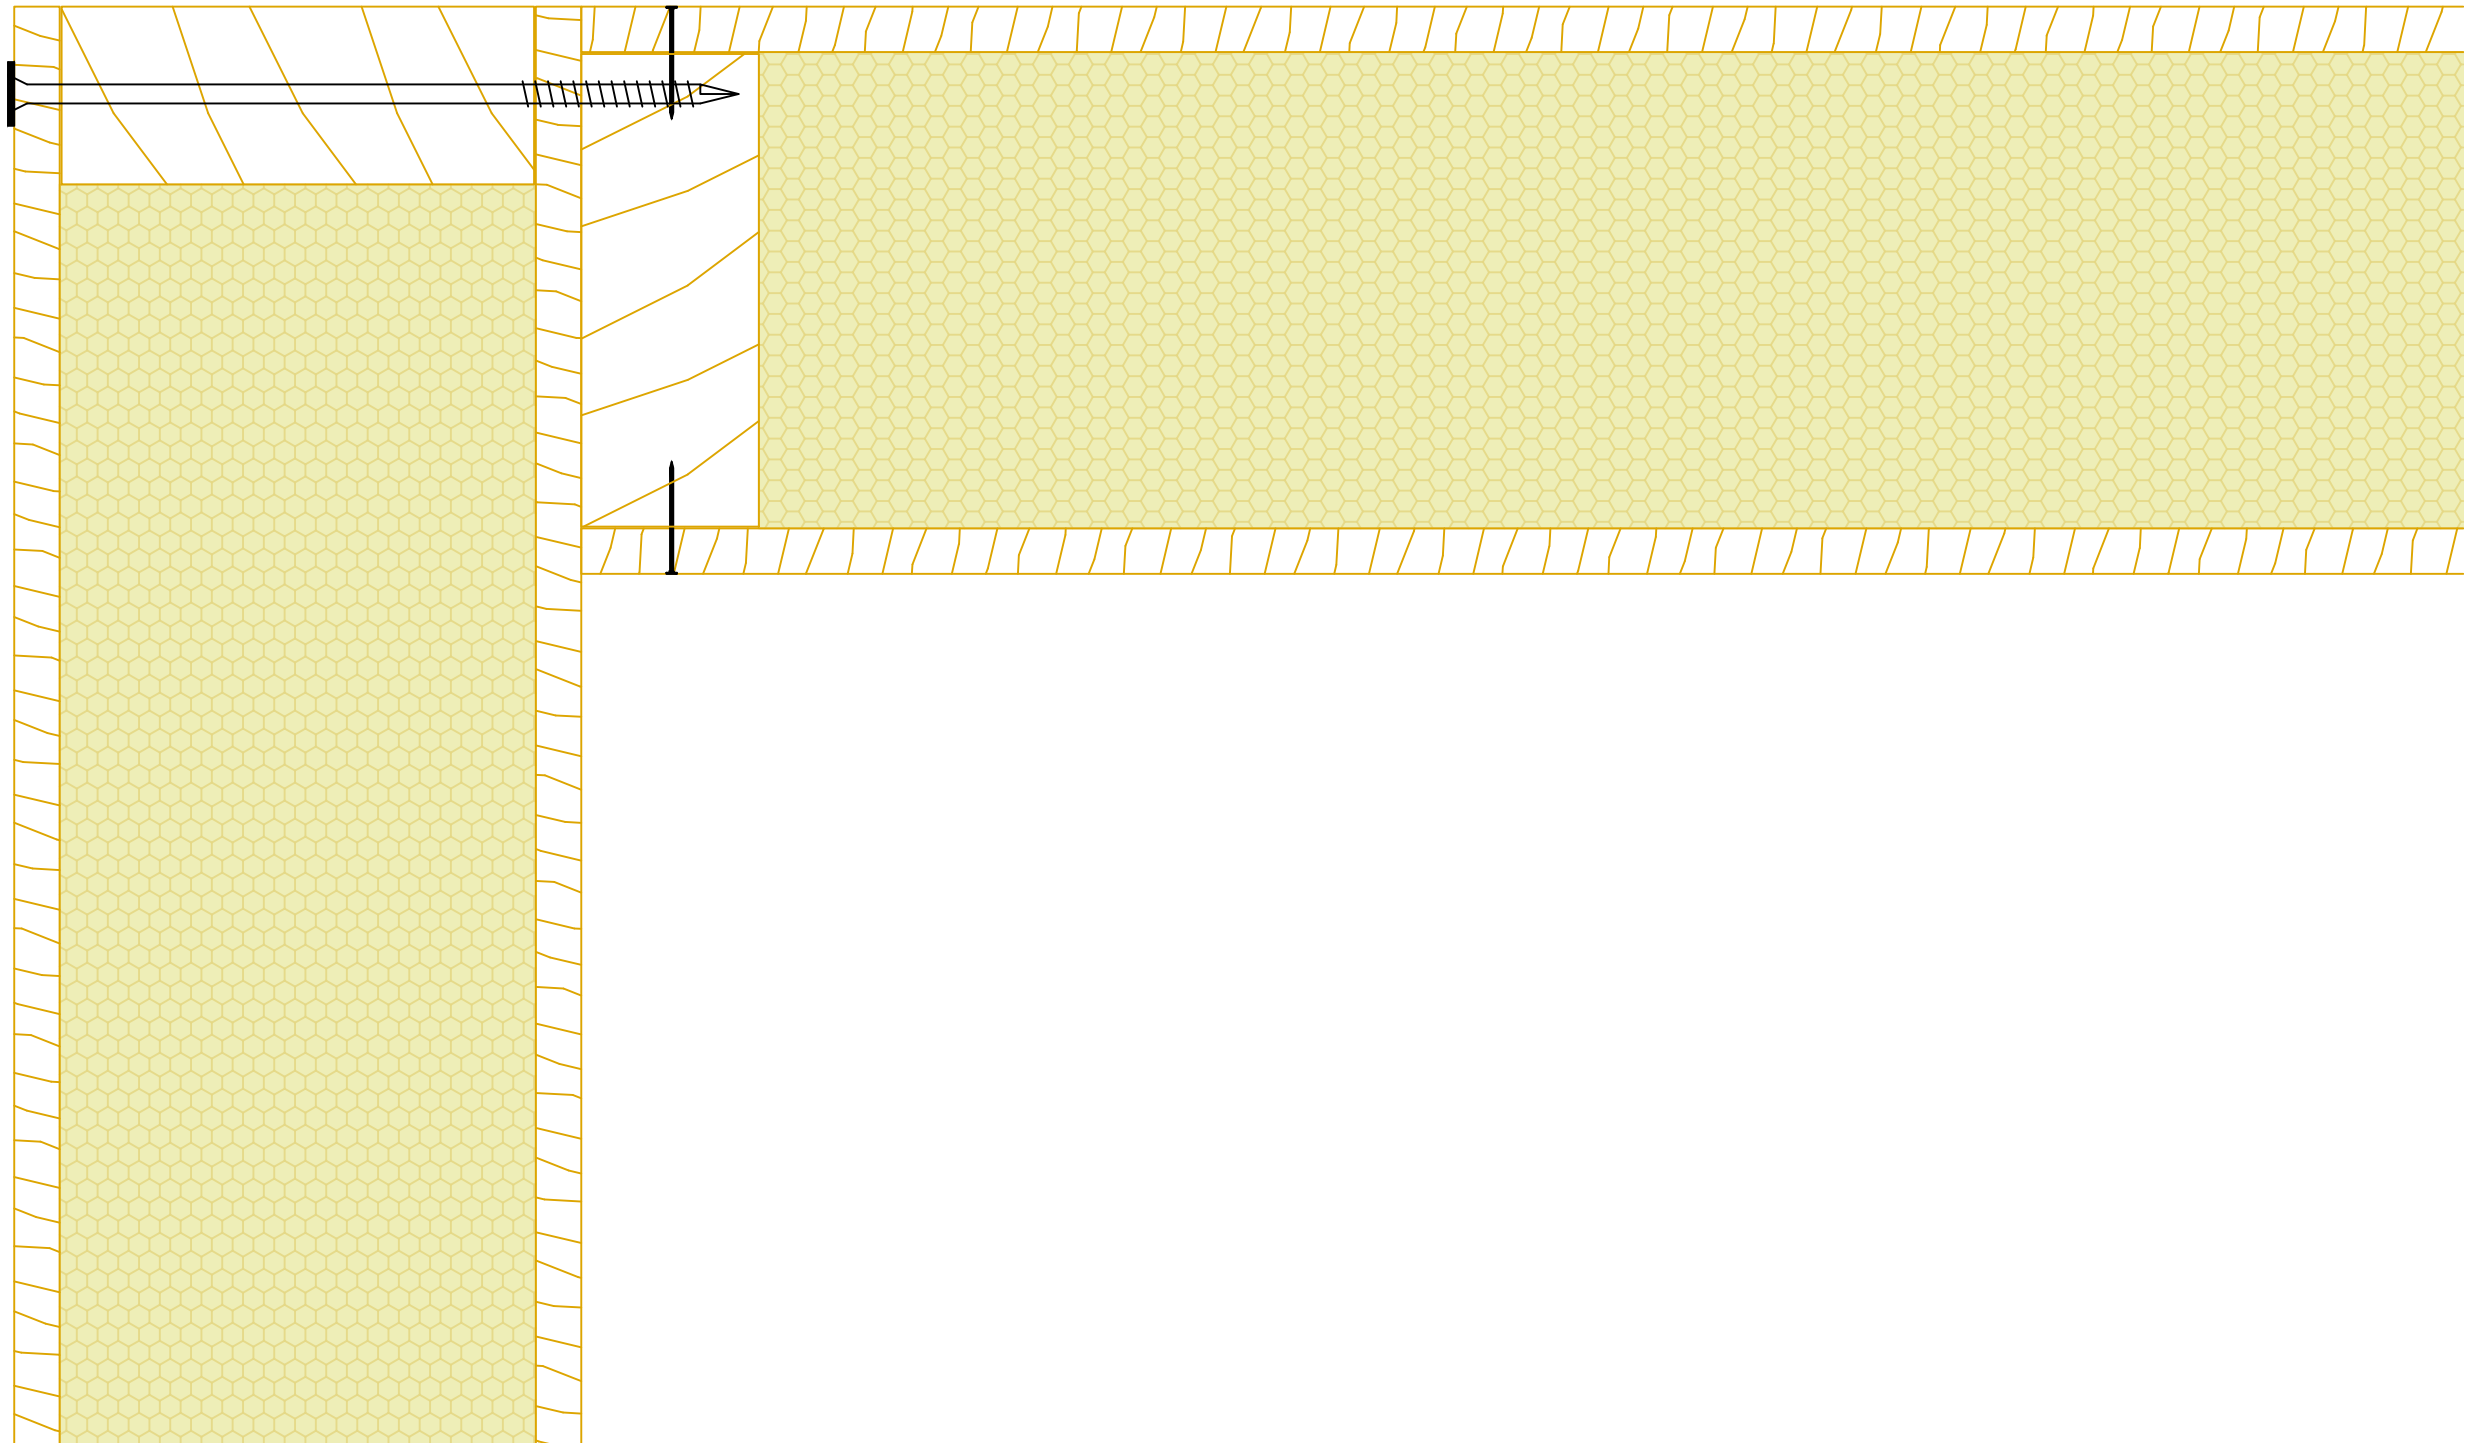

phone: 01590 642 087
e-mail: sales@newforestips.co.uk
web: www.newforestips.co.uk

CORNER JUNCTION