


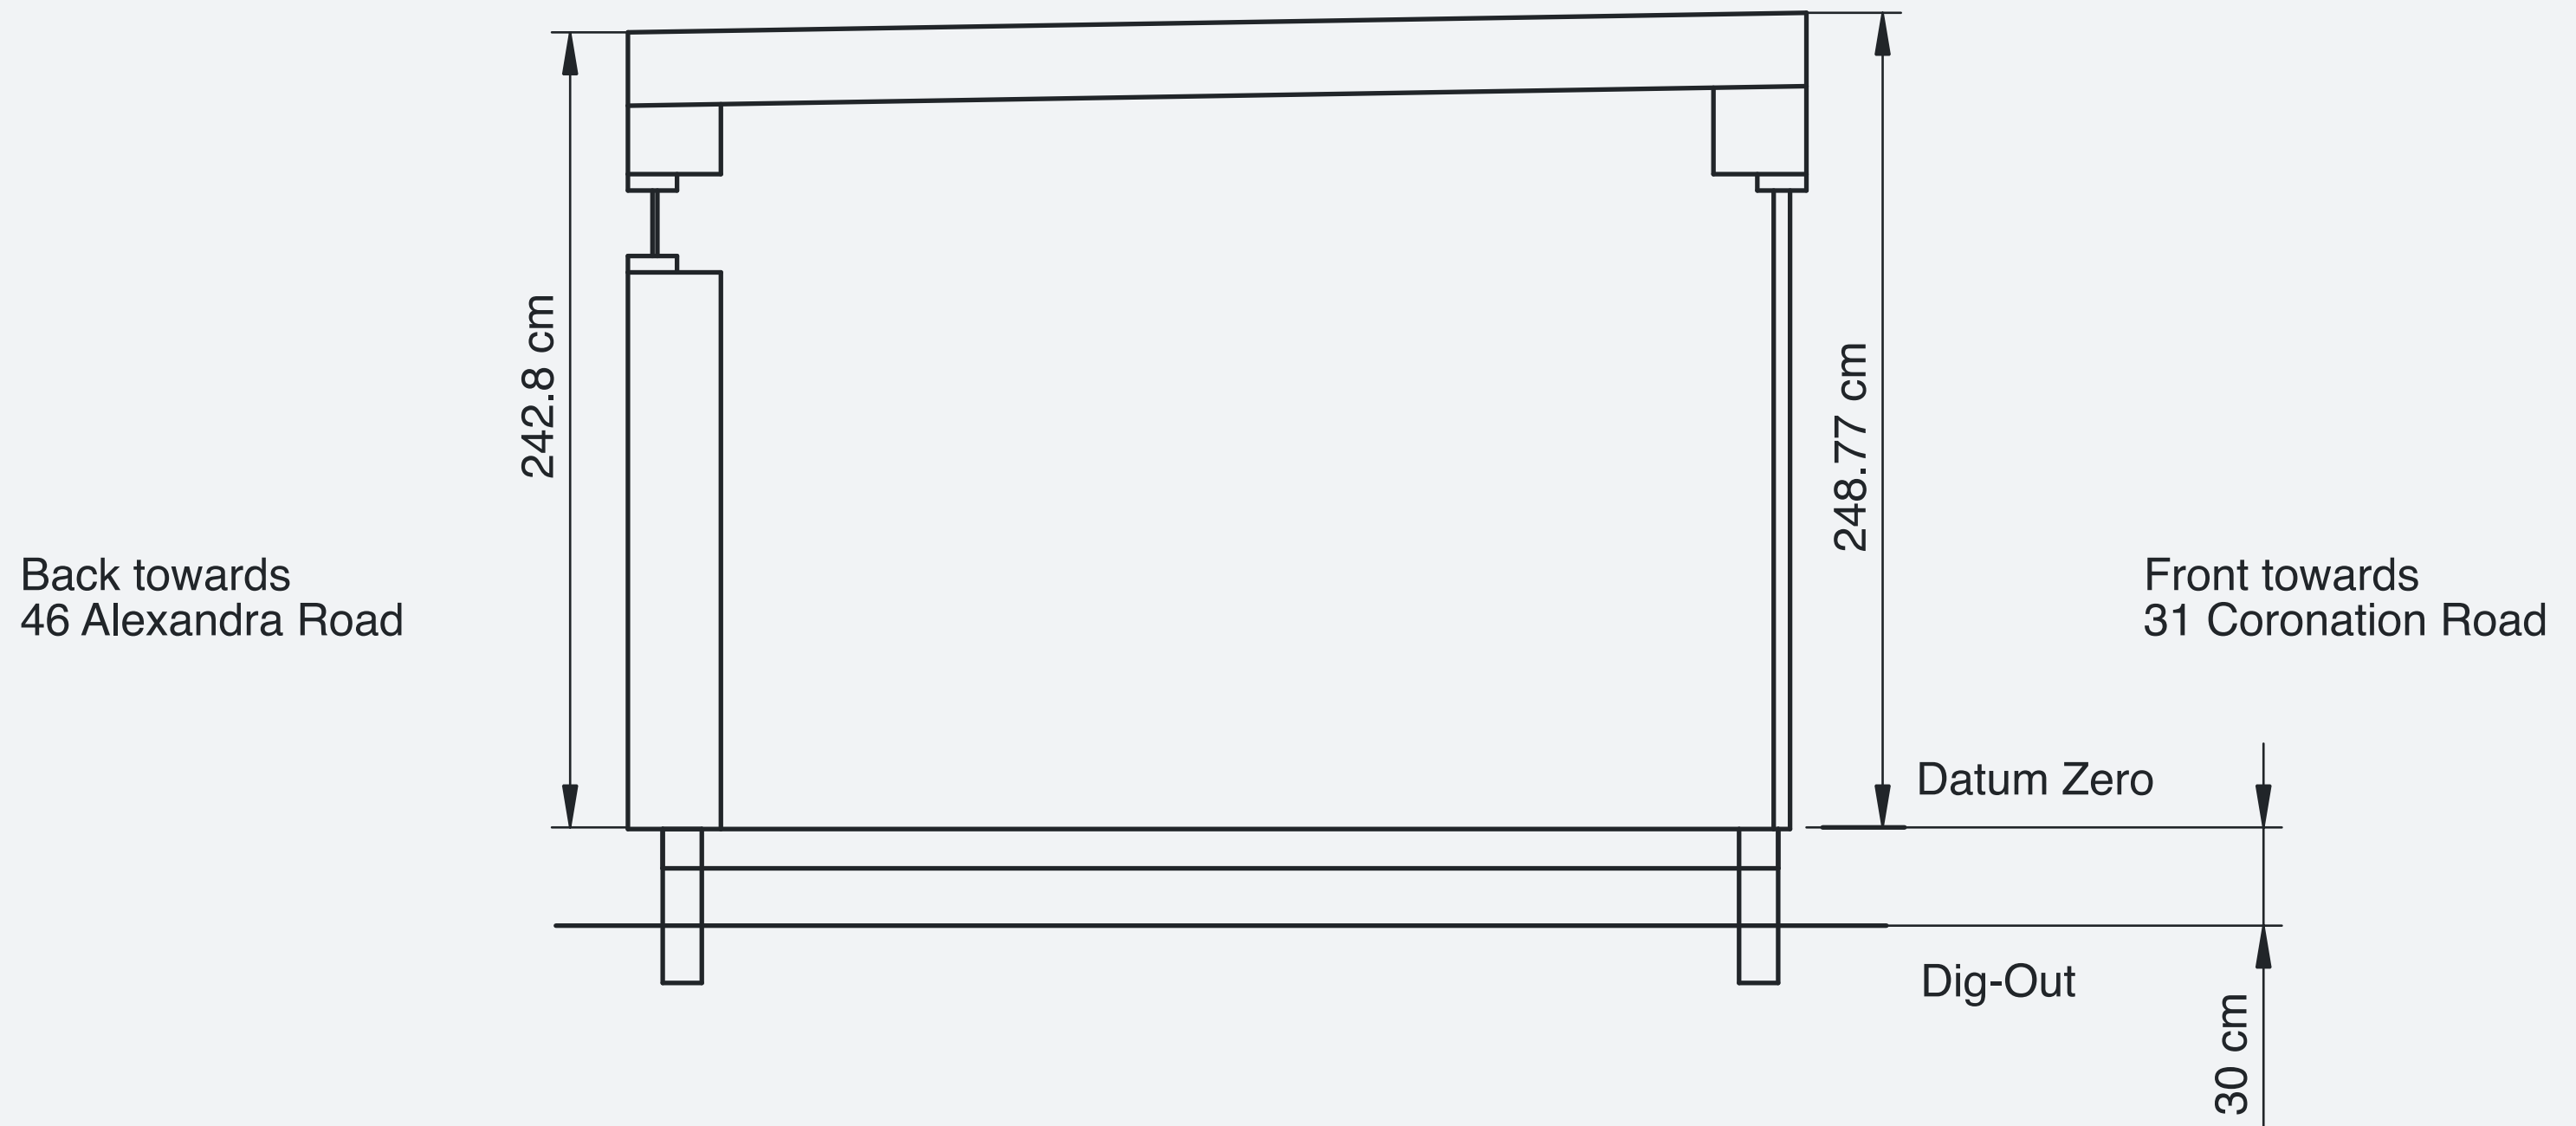

Note: Site is an existing level residential garden. Ground level variation across the 3.6m footprint is negligible (<1 degree). Maximum building height is calculated from the highest adjacent ground level (Datum Zero) to ensure strict compliance with the 2.5m Permitted Development boundary height limit.